| SYMBOL | DESCRIPTION |
|---|---|
| FCP | FIRE ALARM CONTROL PANEL |
| MM | MONITOR MODULE |
| CM | CONTROL MODULE |
| RM | RELAY MODULE |
| ISO | ISOLATOR |
| ANN | GRAPHIC ANNUNCIATOR |
| MTL | MASTER FIRE TELEPHONE |
| FTB | FIRE ALARM TERMINAL BOX |
| PSU | POWER SUPPLY WITH BATTERY BACK UP |
| BC | BEAM DETECTOR CONTROLLER |
| SS | SUPERVISERY SWITCH |
| FS | FLOW SWITCH |
| K B | BEAM DETECTOR |
| H | HEAT DETECTOR,CON |
| S | SMOKE DETECTOR,CON |
| M | MANUAL STATION,CON |
| T | FIRE TELEPHONE JACK |
| SP | SPEAKER WITH STROBE LIGHT |
| L | INDECATOR LAMP |
| Ω | END OF LINE |

หมายเหตุ


1) LSHF = LOW SMOKE HALOGEN FREE CABLE (NON-SHEATHED)
- เป็นสายไฟฟ้าแบบที่มีฉนวนหุ้ม เป็นสายไฟฟ้าที่มีคุณสมบัติต้านทานการลุกลามไฟ ควันน้อย และไม่ปล่อยก๊าซพิษที่มีฤทธิ์เป็นกรดเมื่อสายถูกเผาไหม้ โดยโครงสร้างของสายไฟฟ้าจะต้องเป็นไปตามมาตรฐาน BS EN50525-3-41 และต้องได้รับการทดสอบตามมาตรฐาน IEC 60332-1-2, IEC 60332-3-24 CATEGORY C, IEC 60332-3-22 CATEGORY A, IEC 60754-1, IEC 60754-2 และ IEC 61034-2

2) LSHF-S = LOW SMOKE HALOGEN FREE CABLE (SHEATHED)
- เป็นสายไฟฟ้าแบบที่มีฉนวนและเปลือกหุ้ม เป็นสายไฟฟ้าที่มีคุณสมบัติต้านทานการลุกลามไฟ ควันน้อย และไม่ปล่อยก๊าซพิษที่มีฤทธิ์เป็นกรดเมื่อสายถูกเผาไหม้ โดยโครงสร้างของสายไฟฟ้าจะต้องเป็นไปตามมาตรฐาน IEC 60228, IEC 60502-1 และต้องได้รับการทดสอบตามมาตรฐาน IEC 60332-1-2, IEC 60332-3-24 CATEGORY C, IEC 60332-3-22 CATEGORY A, IEC 60754-1, IEC 60754-2 และ IEC 61034-2


3) FRC = FIRE RESISTANCE CABLE
- เป็นสายไฟฟ้าทนไฟแบบที่มีฉนวนและเปลือกหุ้มโดยโครงสร้างของสายไฟฟ้าจะต้องเป็นไปตามมาตรฐาน IEC 60228, IEC 60502-1 และต้องได้รับการทดสอบตามมาตรฐาน IEC 60332-1-2, IEC 60332-3-24 CATEGORY C, IEC 60332-3-22 CATEGORY A, IEC 60754-1, IEC 60754-2, IEC 61034-2, IEC 60331 และ BS 6387 CATEGORY C,W,Z

หมายเหตุ

งานก่อสร้าง Phase 2

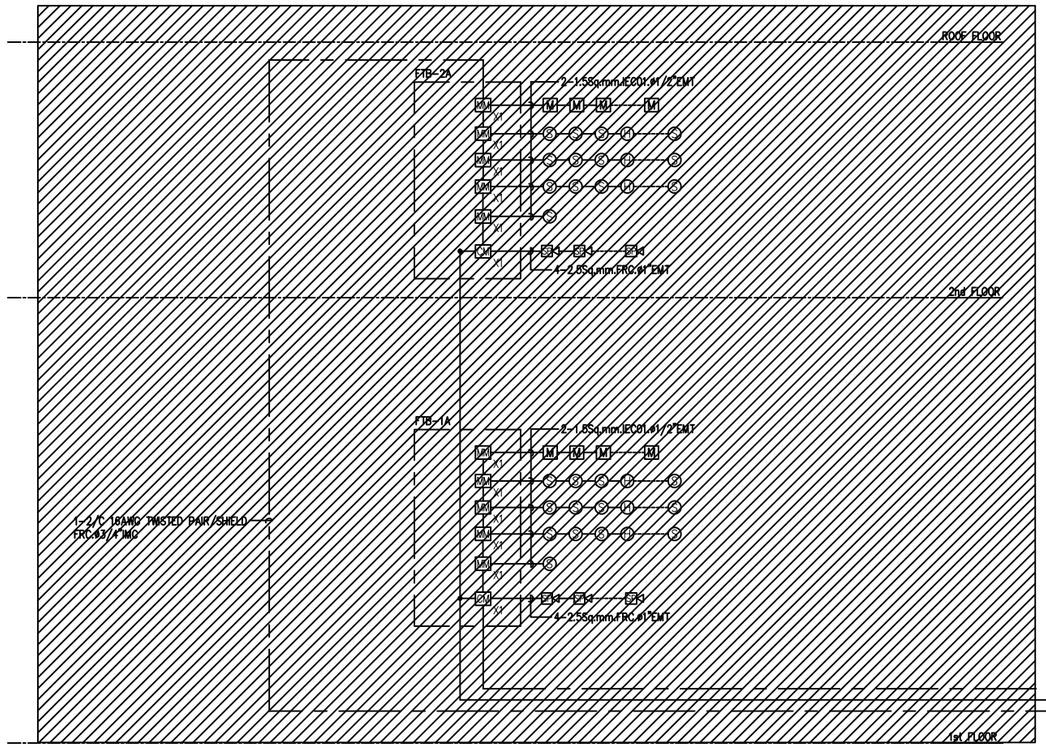


FIRE ALARM SYSTEM RISER DIAGRAM (BUILDING A)
SCALE NTS.

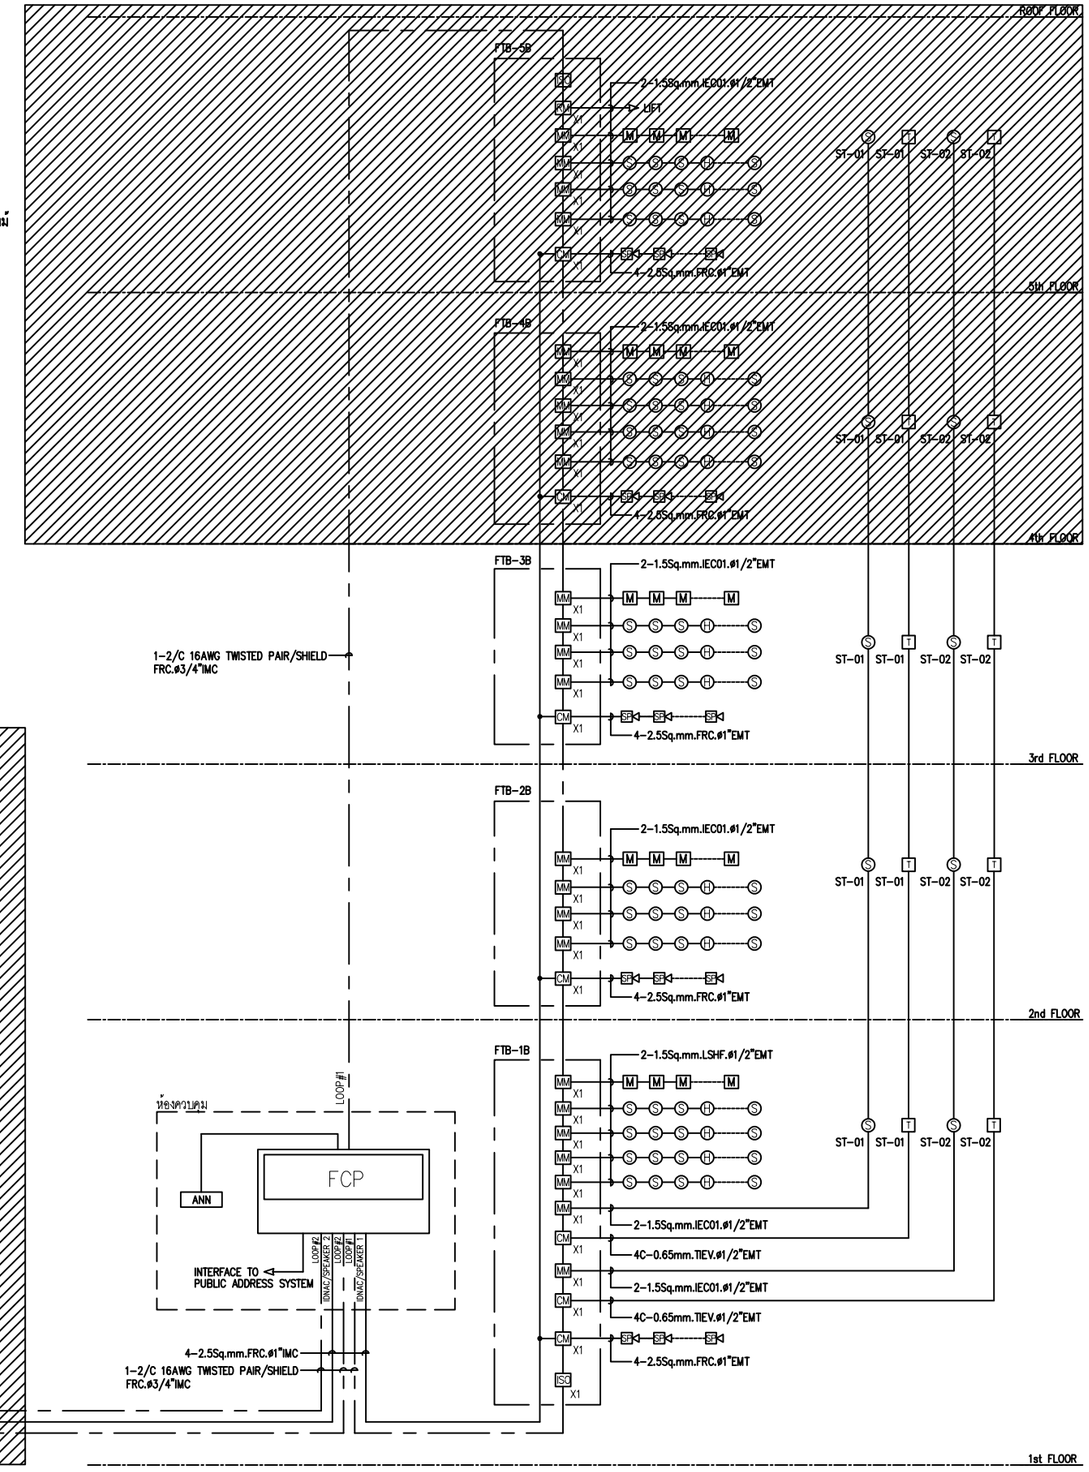


FIRE ALARM SYSTEM RISER DIAGRAM (BUILDING B)
SCALE NTS.

OWNER:
สถาบันเทคโนโลยีพระจอมเกล้าเจ้าคุณทหารลาดกระบัง
เลขที่ 3 หมู่ 2 กรุงเทพมหานคร แขวงลำปลาทิว
เขตลาดกระบัง กทม. 10520

PROJECT:
King Mongkut's
International Demonstration School
ของสถาบันเทคโนโลยีพระจอมเกล้าเจ้าคุณทหารลาดกระบัง
งานก่อสร้างโรงเรียนสาธิตนานาชาติ

ARCHITECT:
นายณกาจ ตำรงค์เกียรติ ส-สถ. 3476
นายสัทธา ปัญญาแก้ว ส-สถ. 3677
นางสาวอธิรญา เนื่องจำนงค์ ภ-สถ.26389
นางสาวกนกวรรณ โพธิ์พิทยา ภ-สถ.26302

STRUCTURAL ENGINEER:
นาย บัณฑิต อยู่เยาว์ สย. 12188

SANITARY ENGINEER:
นาย ธนเดช ไชยวรรณ ภส. 1475

ELECTRICAL ENGINEER:
นาย รุ่ง แสงศรี วฟท.1510
นาย สุริยา ขรรค์บริวาร สฟท.3053
นาย เกรียงไกร สุชรัตน์ ภฟท.52841

MECHANICAL ENGINEER:
นาย ธนเดช ไชยวรรณ วก.1242

LANDSCAPE :
นาย อนันต์ อนันตวงศ์ ภภส. 276

KEY PLAN:

| REV. | DATE | ISSUED / DESCRIPTION |
|---|---|---|
| | | |

DRAWN BY : -
CHECKED BY :

DRAWING TITLE: FIRE ALARM SYSTEM RISER DIAGRAM

DRAWING NO: EE-08

NOTE:

SCALE: A3 1:250
A1 1:125