



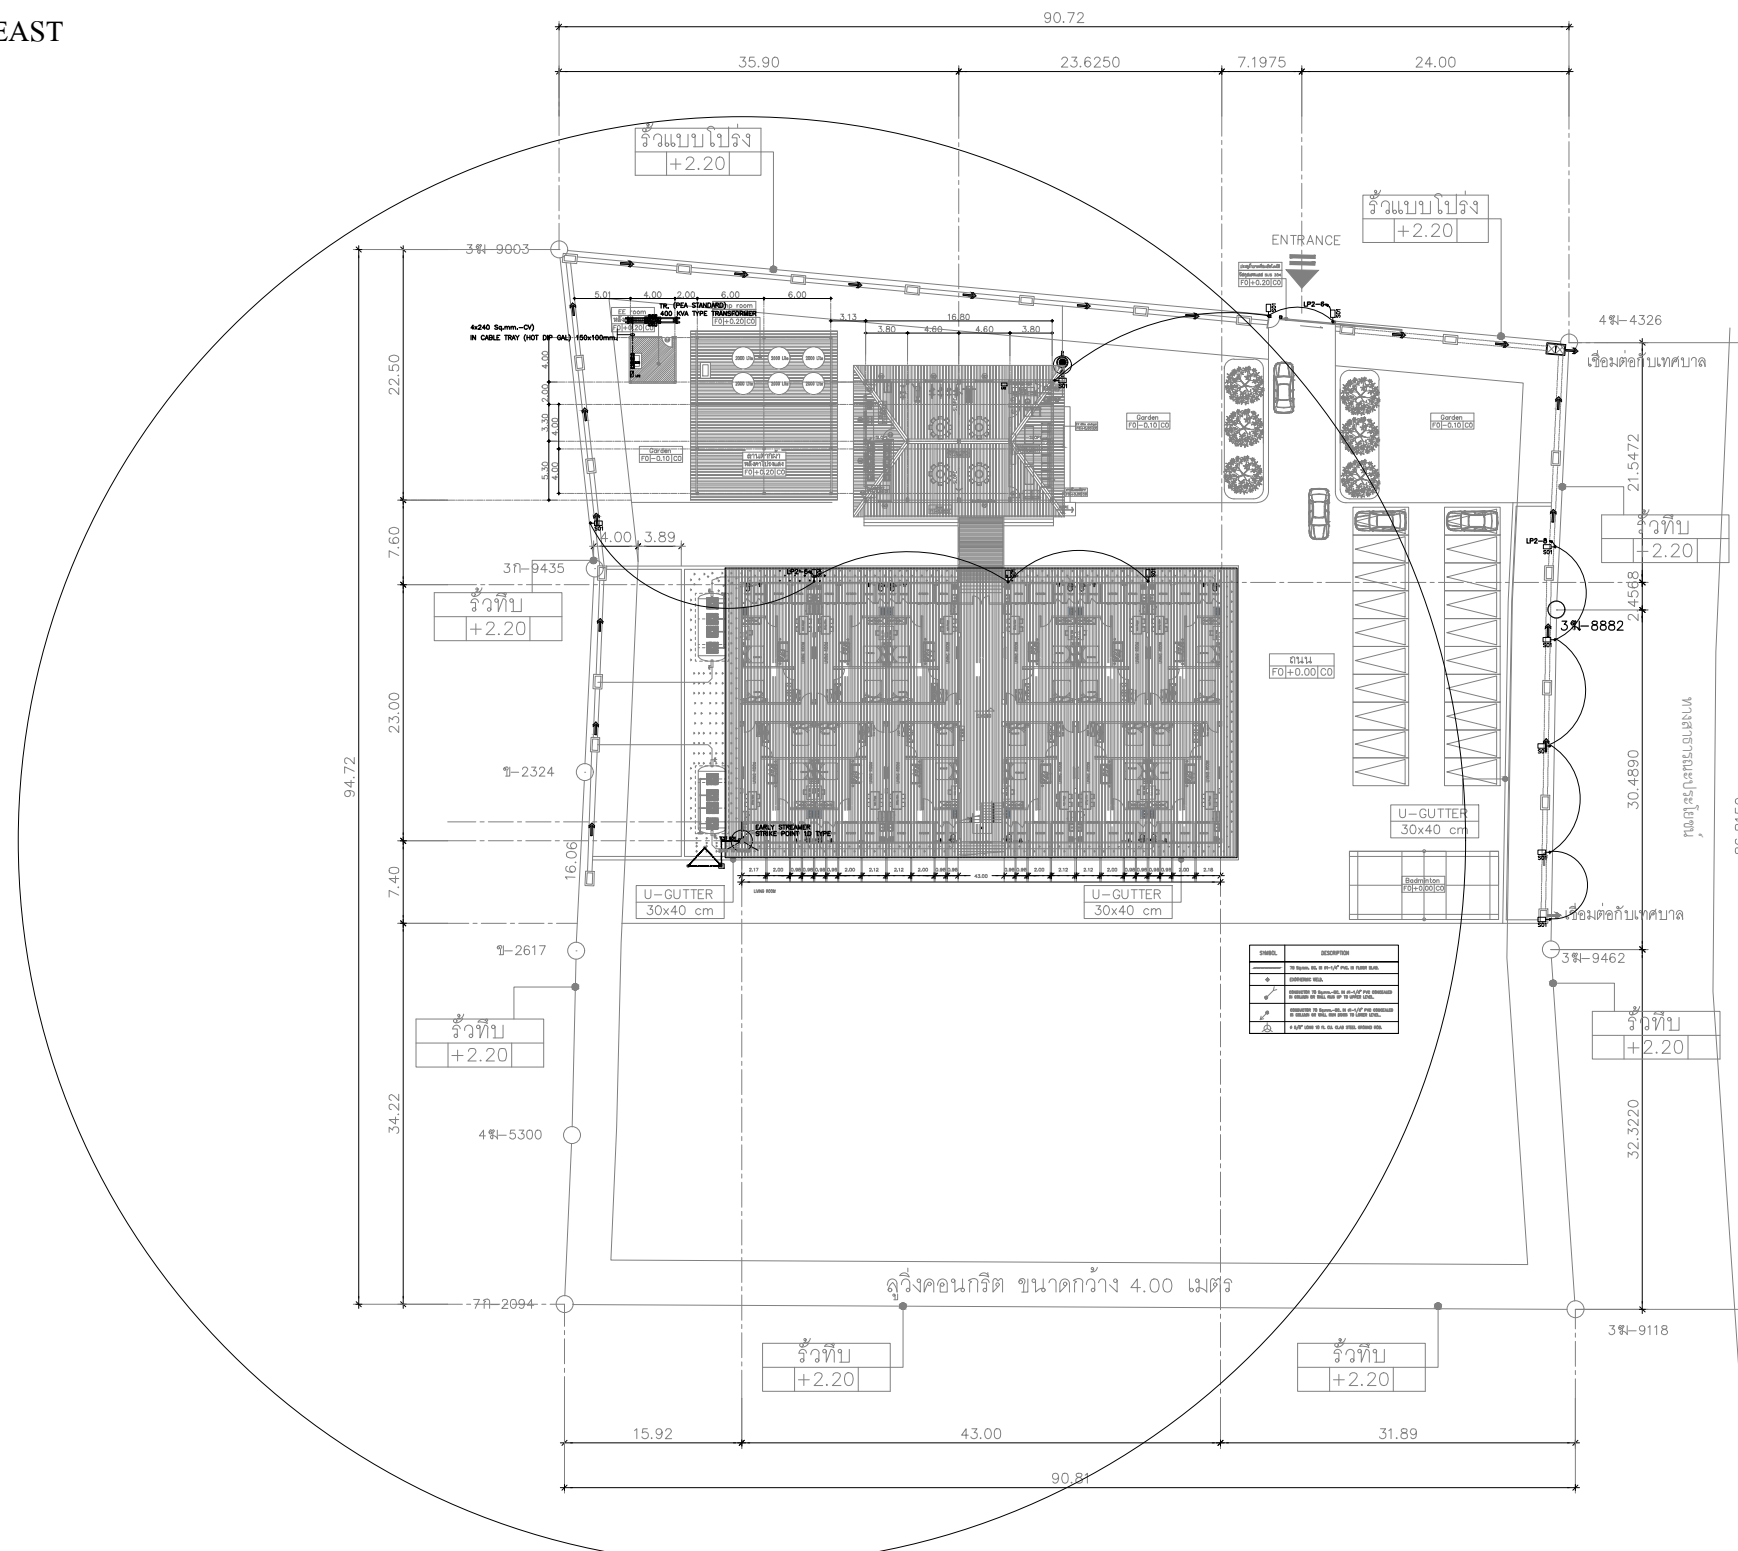

Site Plan Main Electrical & Grounding Plan — 1 st Floor

Scale

1: 400

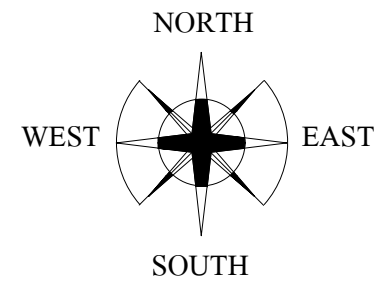




PROJECT :
2-storey apartment
(Building A)

OWNER :
UNITECH PCB (THAILAND)
LOCATION :
Chorakhe Rong Chaiyo Ang Thong Province, Thailand

STRUCTURAL ENGINEER : นายชานนท์ สงนวนงษ์ สย. 4227
333 หมู่ 3 ต.ปากคลองบางปลากด อ.พระสมุทรเจดีย์ จ.สมุทรปราการ
ARCHITECT : นายสุรชัย วาณิช ส.ส. 3003
139/13 ซอยลาดพร้าว 41 แขวงจันทรมาน เขตจตุจักร กรุงเทพมหานคร

ELECTRICAL ENGINEER :
SANITARY ENGINEER :

DRAWING NO. :
EE-001
REMARK :
FOR CONSTRUCTION

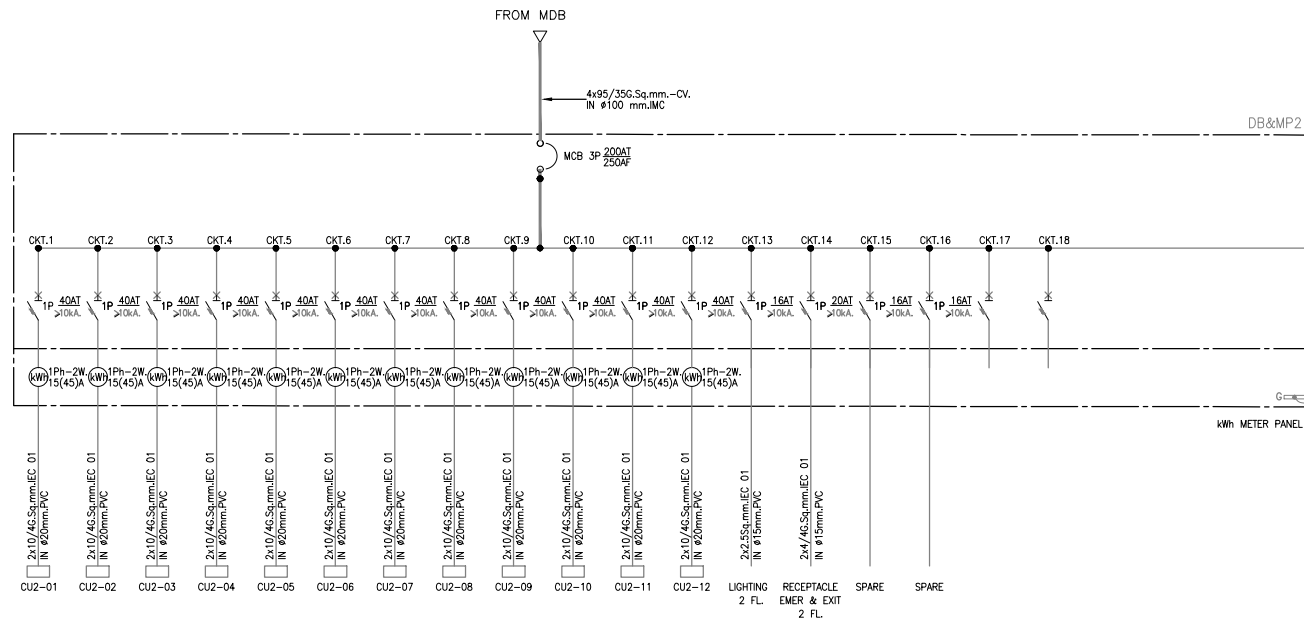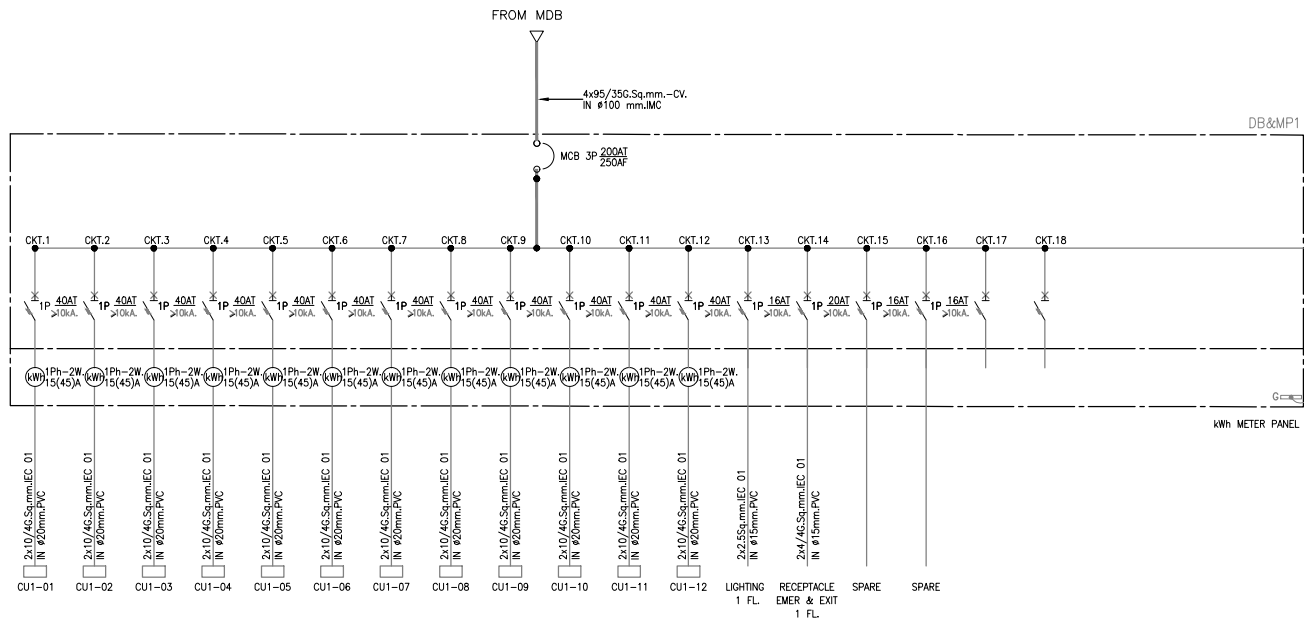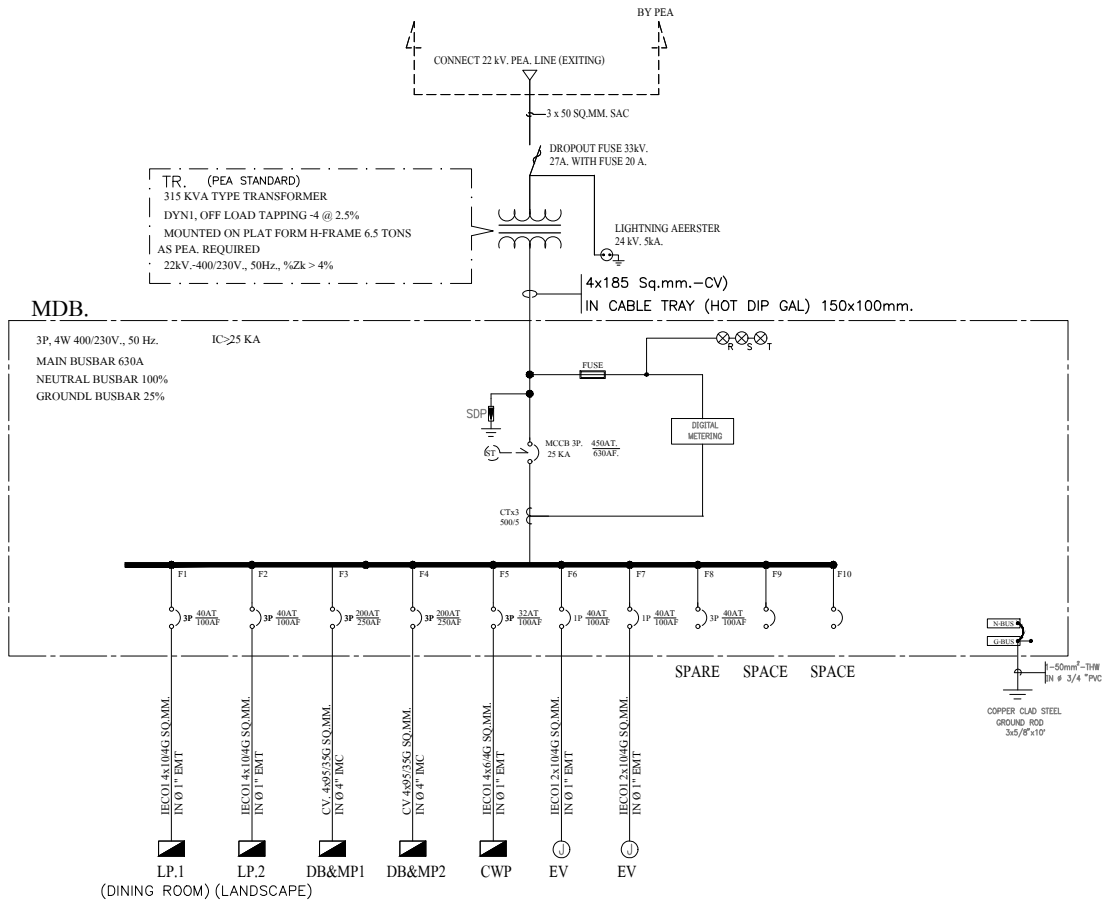

SINGLE LINE DIAGRAM MDB&DB

มาตรฐาน

1:100




PROJECT :
2-storey apartment
(Building A)



OWNER :
UNITECH PCB (THAILAND)
LOCATION :
Chorakhe Rong Chaiyo Ang Thong Province, Thailand

STRUCTURAL ENGINEER : นายชานนท์ สงนวนงษ์ สย 4227
333 หมู่ 3 ต.ปากคลองบางปลากด อ.พระสมุทรเจดีย์ จ.สมุทรปราการ
ARCHITECT : นายสุรชัย วานิชดี ส-สด 3003
139/13 ซอยลาดพร้าว 41 แขวงจันทราภิรม เขตจตุจักร กรุงเทพมหานคร

ELECTRICAL ENGINEER :
SANITARY ENGINEER :
DRAWING NO. :
EE-002
REMARK :
FOR CONSTRUCTION

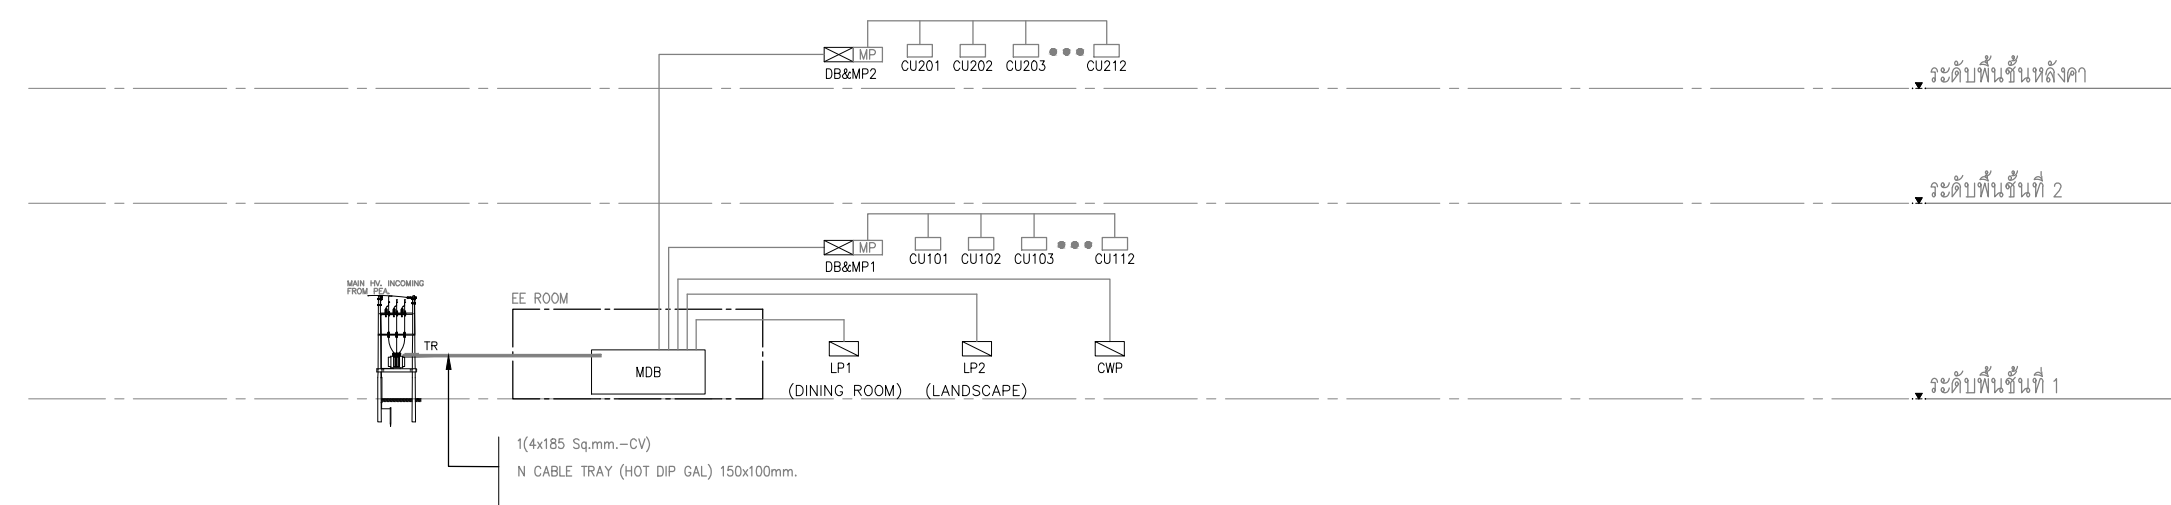


NTS.
ได้คะแนนรวมแล้ว
ได้คะแนนรวมแล้ว

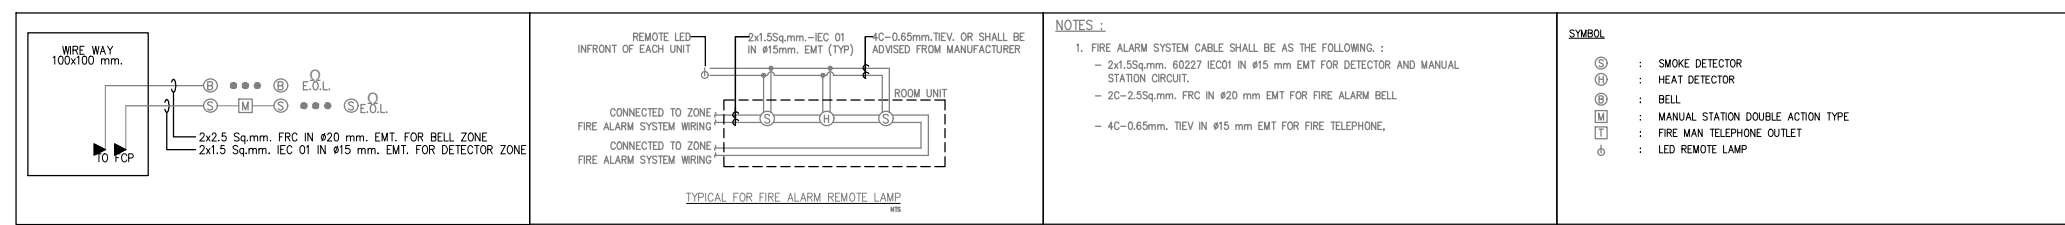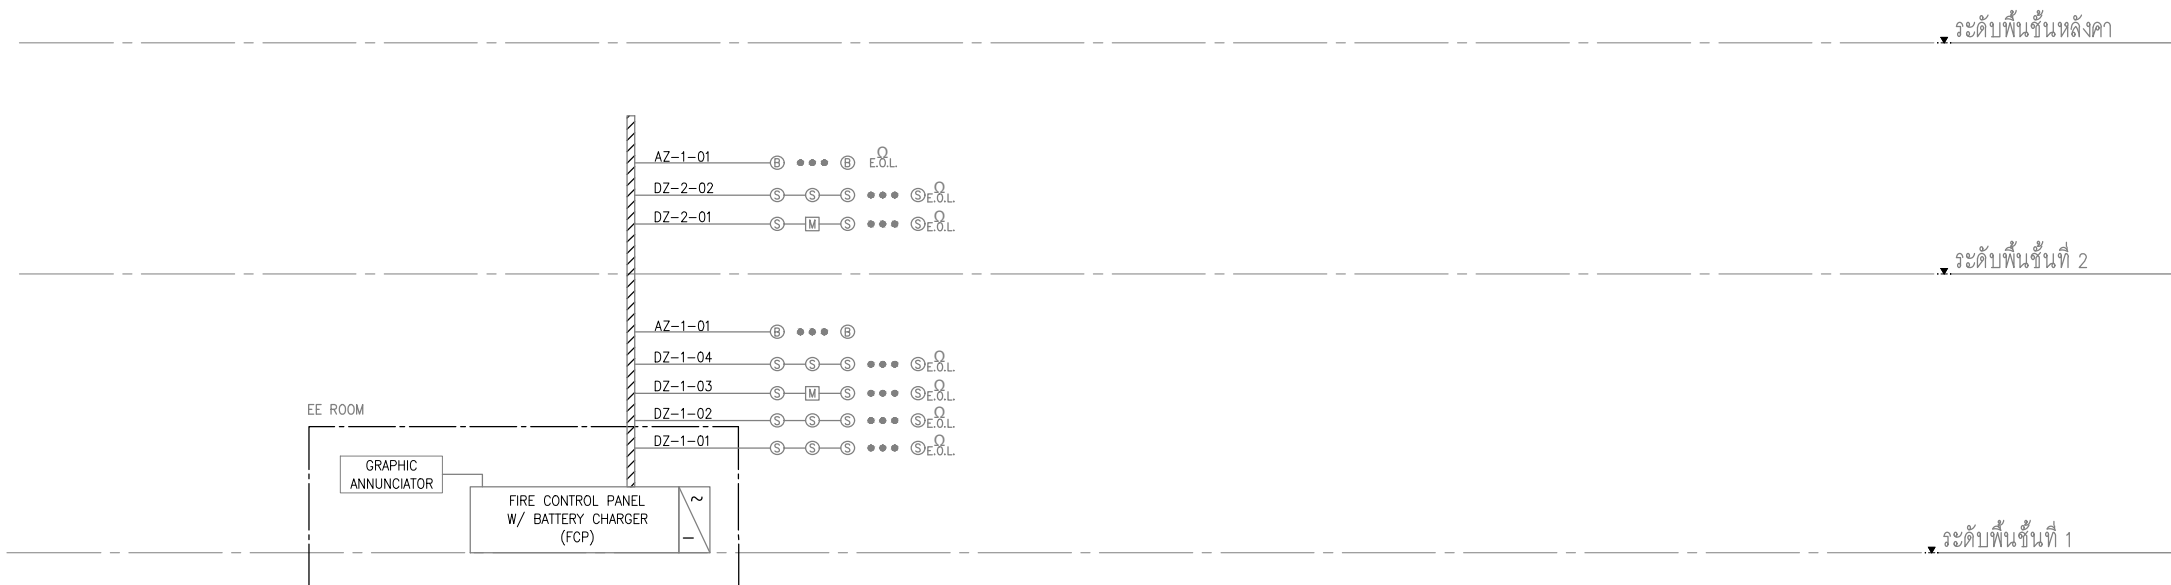


NTS.
ได้คะแนนรวมแล้ว
ได้คะแนนรวมแล้ว

	PROJECT : 2-storey apartment (Building A)	OWNER : UNITECH PCB (THAILAND)	STRUCTURAL ENGINEER : นายชานนท์ สงวนวงศ์ สย 4227	ELECTRICAL ENGINEER :	DRAWING NO. : EE-003
		LOCATION : Chorakhe Rong Chaiyo Ang Thong Province, Thailand	333 หมู่ 3 ต.ปากคลองบางลาดก อ.พระสมุทรเจดีย์ จ.สมุทรปราการ ARCHITECT : นายสุรชัย วาณิช ส-สด 3003 139/13 ซอยลาดพร้าว 41 แขวงจันทรมาน เขตจตุจักร กรุงเทพมหานคร	SANITARY ENGINEER :	REMARK : FOR CONSTRUCTION

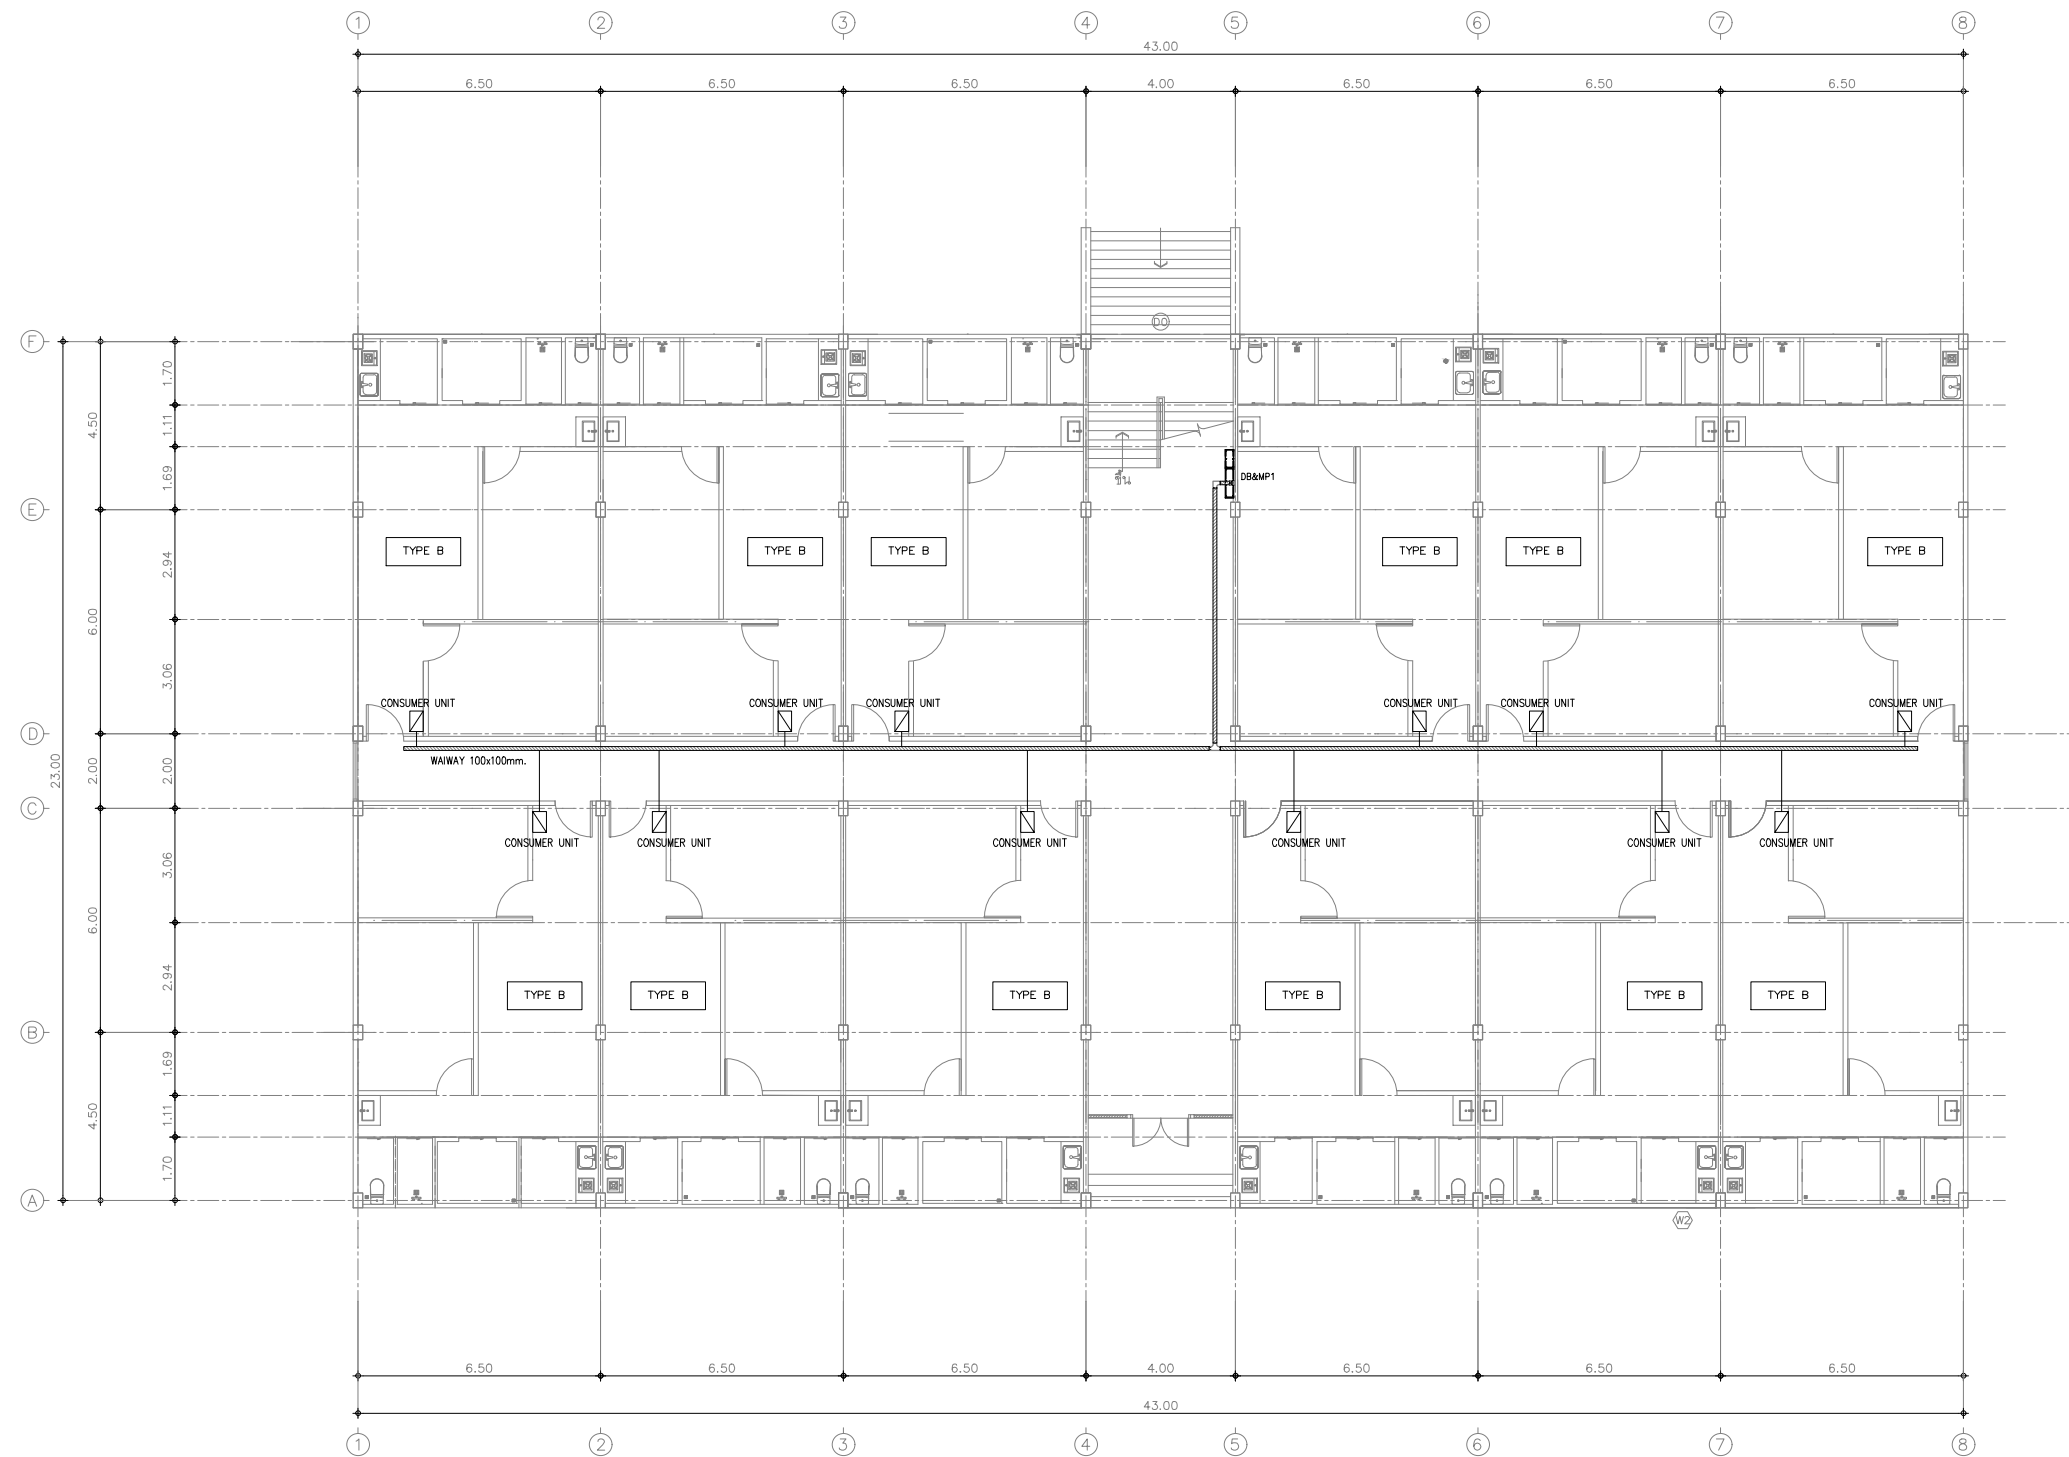

1 ST Floor Main Electrical Plan
Scale 1:100

	PROJECT : 2-storey apartment (Building A)	OWNER : UNITECH PCB (THAILAND)	STRUCTURAL ENGINEER : นายชานนท์ สงวนวงศ์ สย 4227 333 หมู่ 3 ต.ปากคลองบางปลากด อ.พระสมุทรเจดีย์ จ.สมุทรปราการ	ELECTRICAL ENGINEER :	DRAWING NO. : EE-004
		LOCATION : Chorakhe Rong Chaiyo Ang Thong Province, Thailand	ARCHITECT : นายสุรชัย วาณิช ส-สจ 3003 139/13 ซอยลาดพร้าว 41 แขวงจันทน์เกษม เขตจตุจักร กรุงเทพมหานคร	SANITARY ENGINEER :	REMARK : FOR CONSTRUCTION

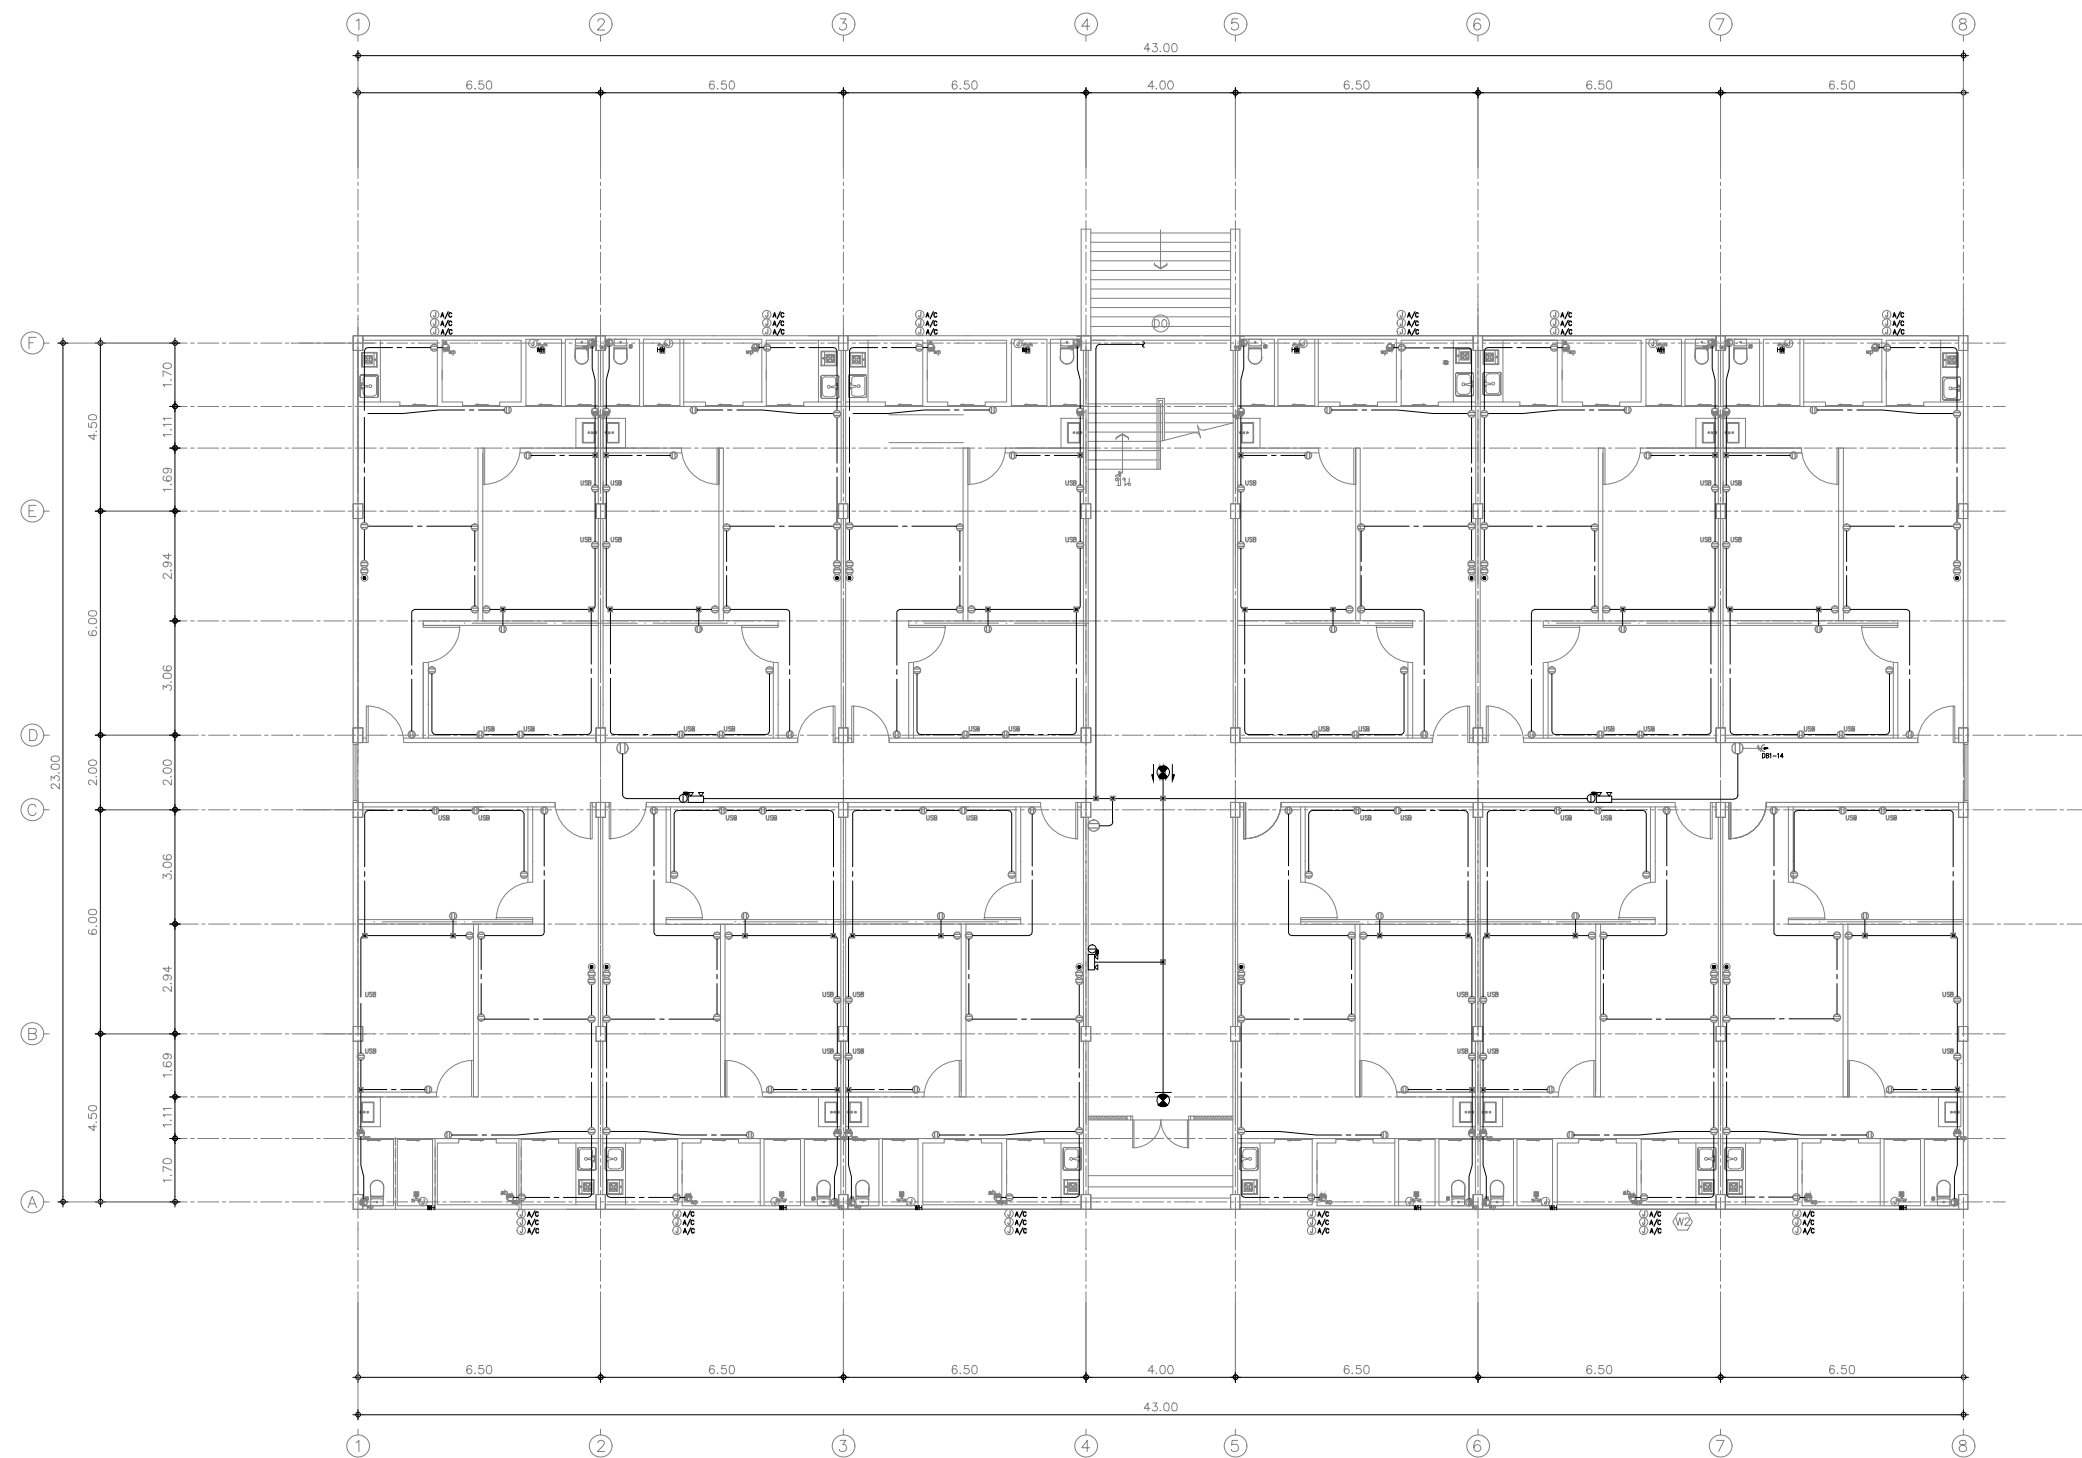

1 ST Floor Power Outlet Plan
Scale 1:100




PROJECT :
2-storey apartment
(Building A)

OWNER :
UNITECH PCB (THAILAND)
LOCATION :
Chorakhe Rong Chaiyo Ang Thong Province, Thailand

STRUCTURAL ENGINEER : นายชานนท์ สงวนวงศ์ สย 4227
333 หมู่ 3 ต.ปากคลองบางปลากด อ.พระสมุทรเจดีย์ จ.สมุทรปราการ
ARCHITECT : นายสุรชัย วาณิช ส-สด 3003
139/13 ซอยลาดพร้าว 41 แขวงจันทราภิรม เขตจตุจักร กรุงเทพมหานคร


ELECTRICAL ENGINEER :
SANITARY ENGINEER :

DRAWING NO. :
EE-005
REMARK :
FOR CONSTRUCTION

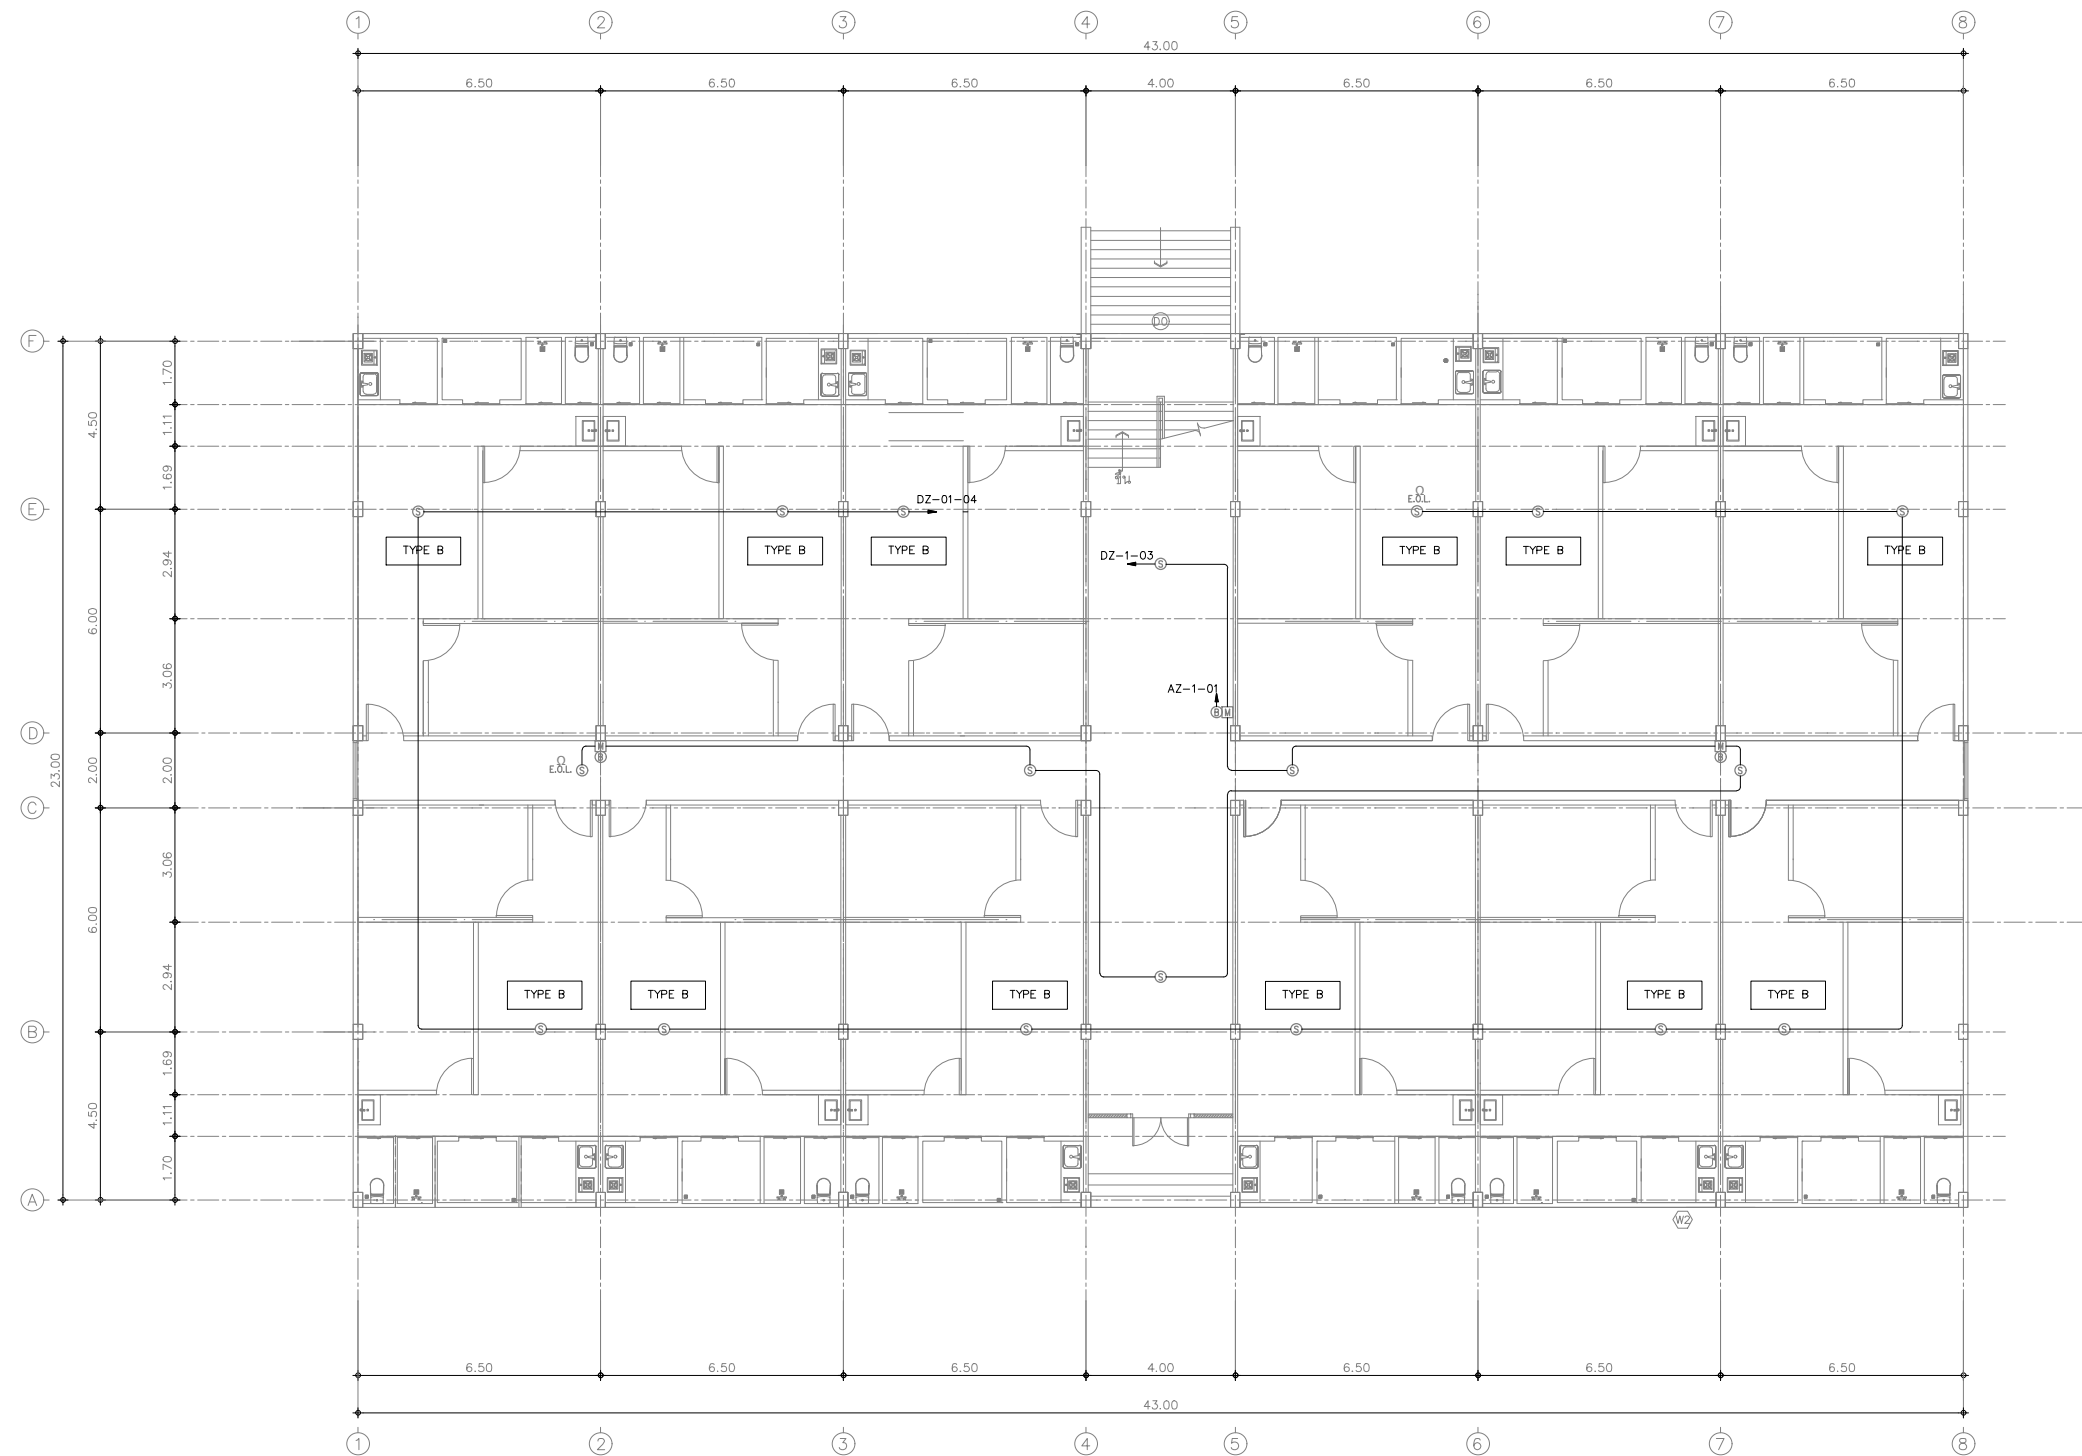

1 ST Floor Fire Alarm Plan
Scale 1:100

	PROJECT : 2-storey apartment (Building A)	OWNER : UNITECH PCB (THAILAND)	STRUCTURAL ENGINEER : นายชานนท์ สงวนวงษ์ สย. 4227 333 หมู่ 3 ต.ปากคลองบางปลากด อ.พระสมุทรเจดีย์ จ.สมุทรปราการ	ELECTRICAL ENGINEER :	DRAWING NO. : EE-006
		LOCATION : Chorakhe Rong Chaiyo Ang Thong Province, Thailand	ARCHITECT : นายสุรชัย วาณิช ส-สจ 3003 139/13 ซอยลาดพร้าว 41 แขวงจันทราภิรม เขตจตุจักร กรุงเทพมหานคร	SANITARY ENGINEER :	REMARK : FOR CONSTRUCTION

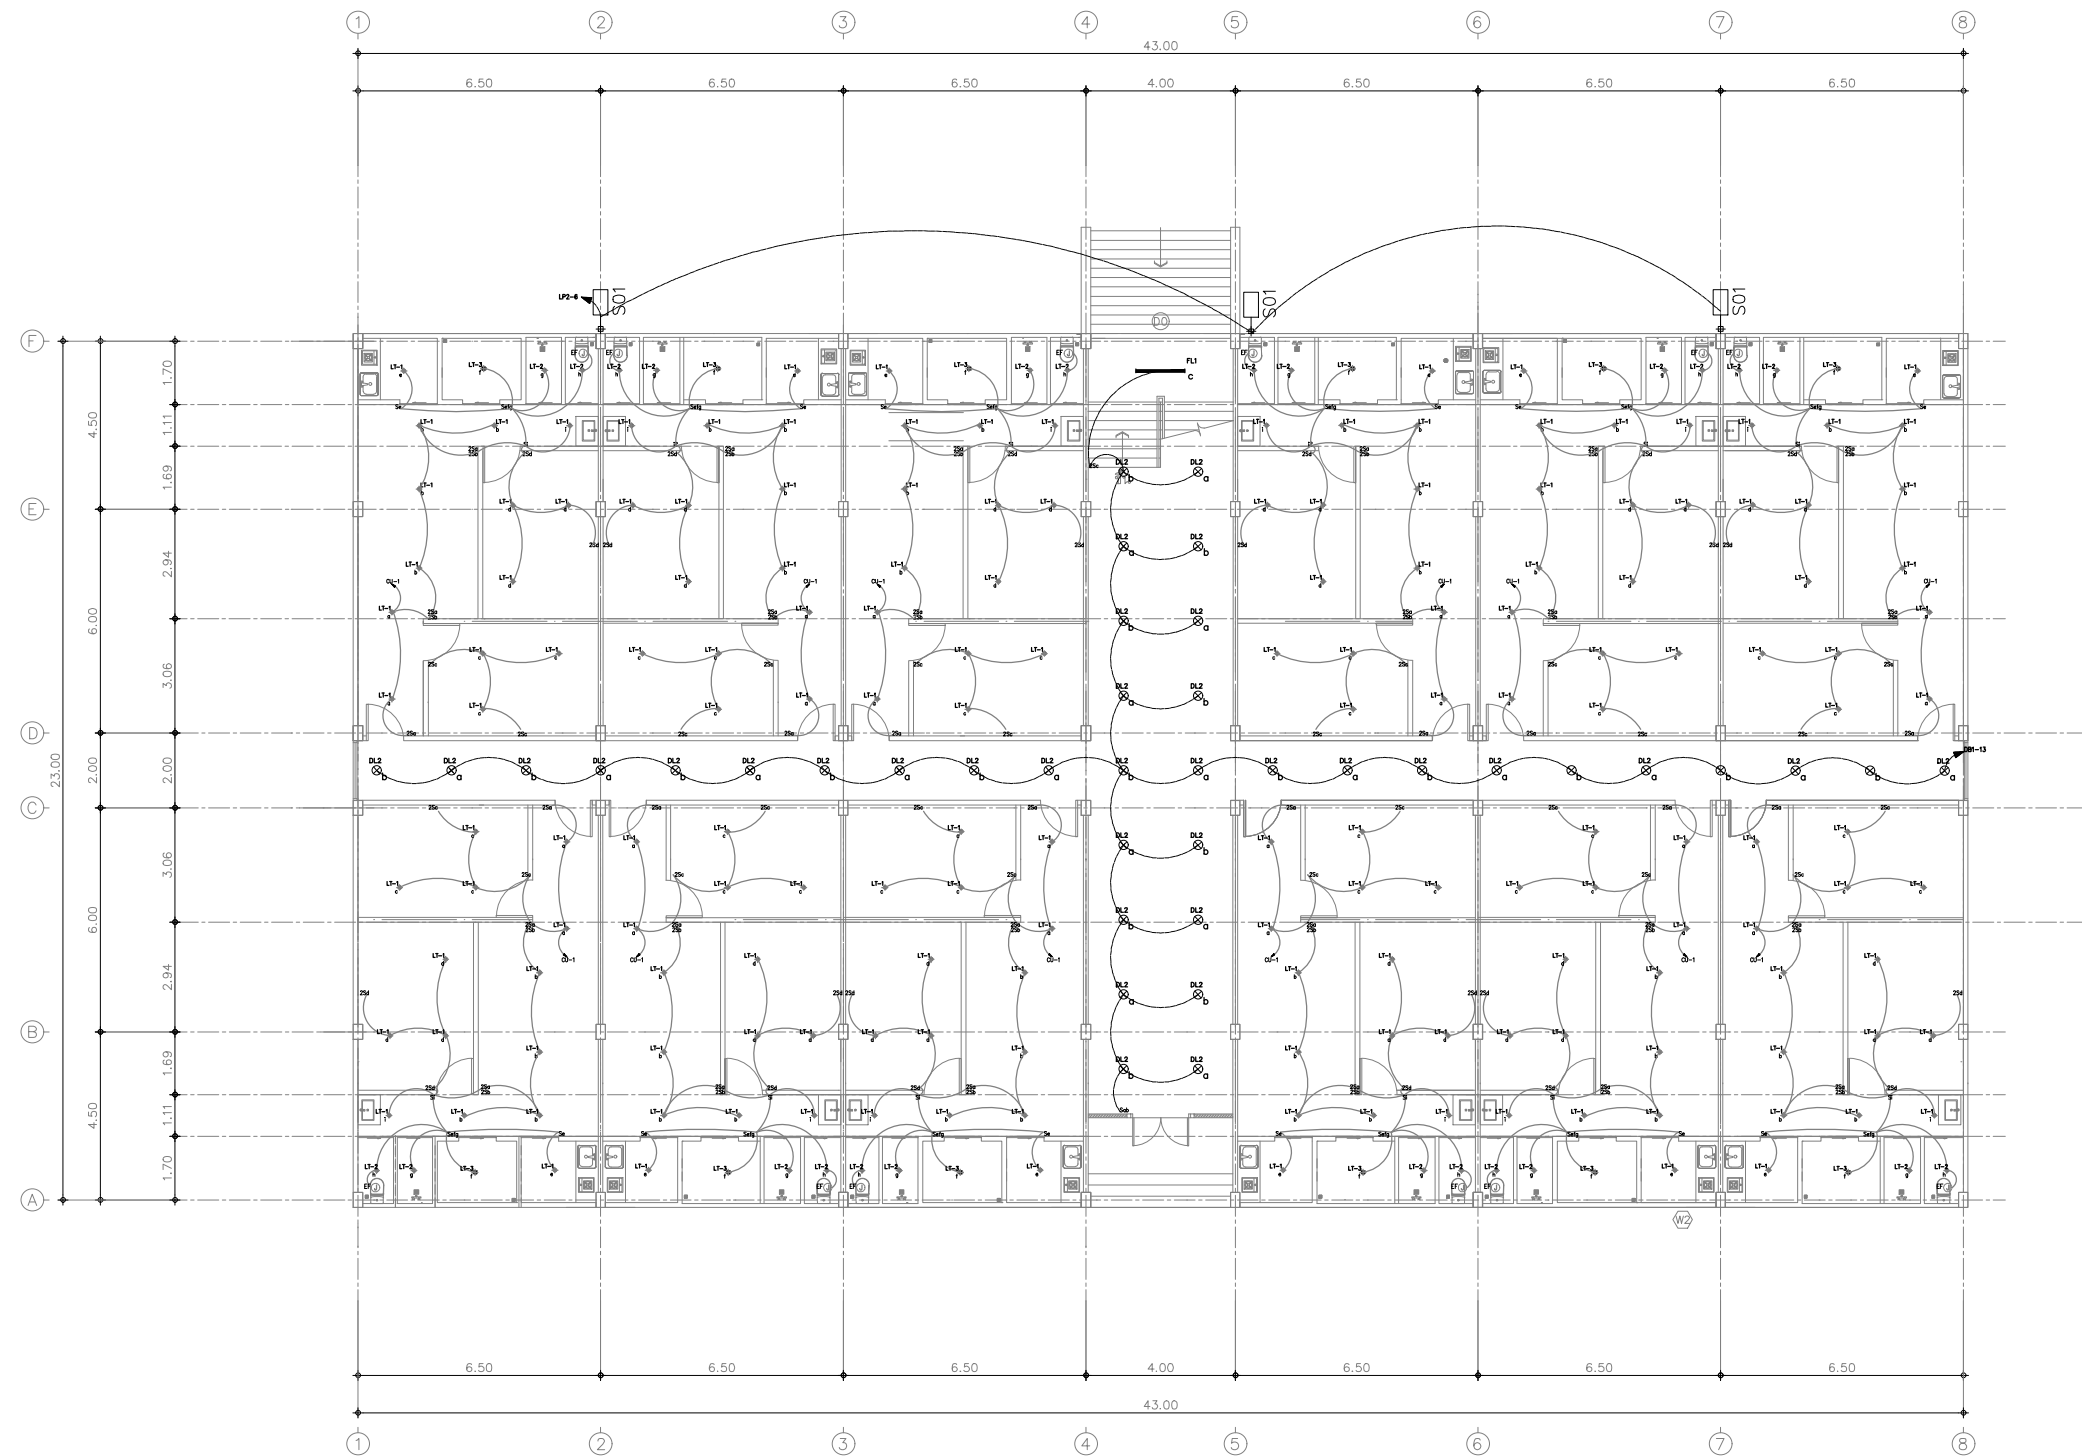

1 ST Floor Lighting Plan

Scale 1:100




PROJECT :
2-storey apartment
(Building A)

OWNER :
UNITECH PCB (THAILAND)
LOCATION :
Chorakhe Rong Chaiyo Ang Thong Province, Thailand

STRUCTURAL ENGINEER : นายชานนท์ สงวนวงษ์ สย 4227
333 หมู่ 3 ต.ปากคลองบางปลากด อ.พระสมุทรเจดีย์ จ.สมุทรปราการ
ARCHITECT : นายสุรชัย วานิชดี ส-สด 3003
139/13 ซอยลาดพร้าว 41 แขวงจันทราภิรม เขตจตุจักร กรุงเทพมหานคร

ELECTRICAL ENGINEER :
SANITARY ENGINEER :

DRAWING NO. :
EE-007
REMARK :
FOR CONSTRUCTION

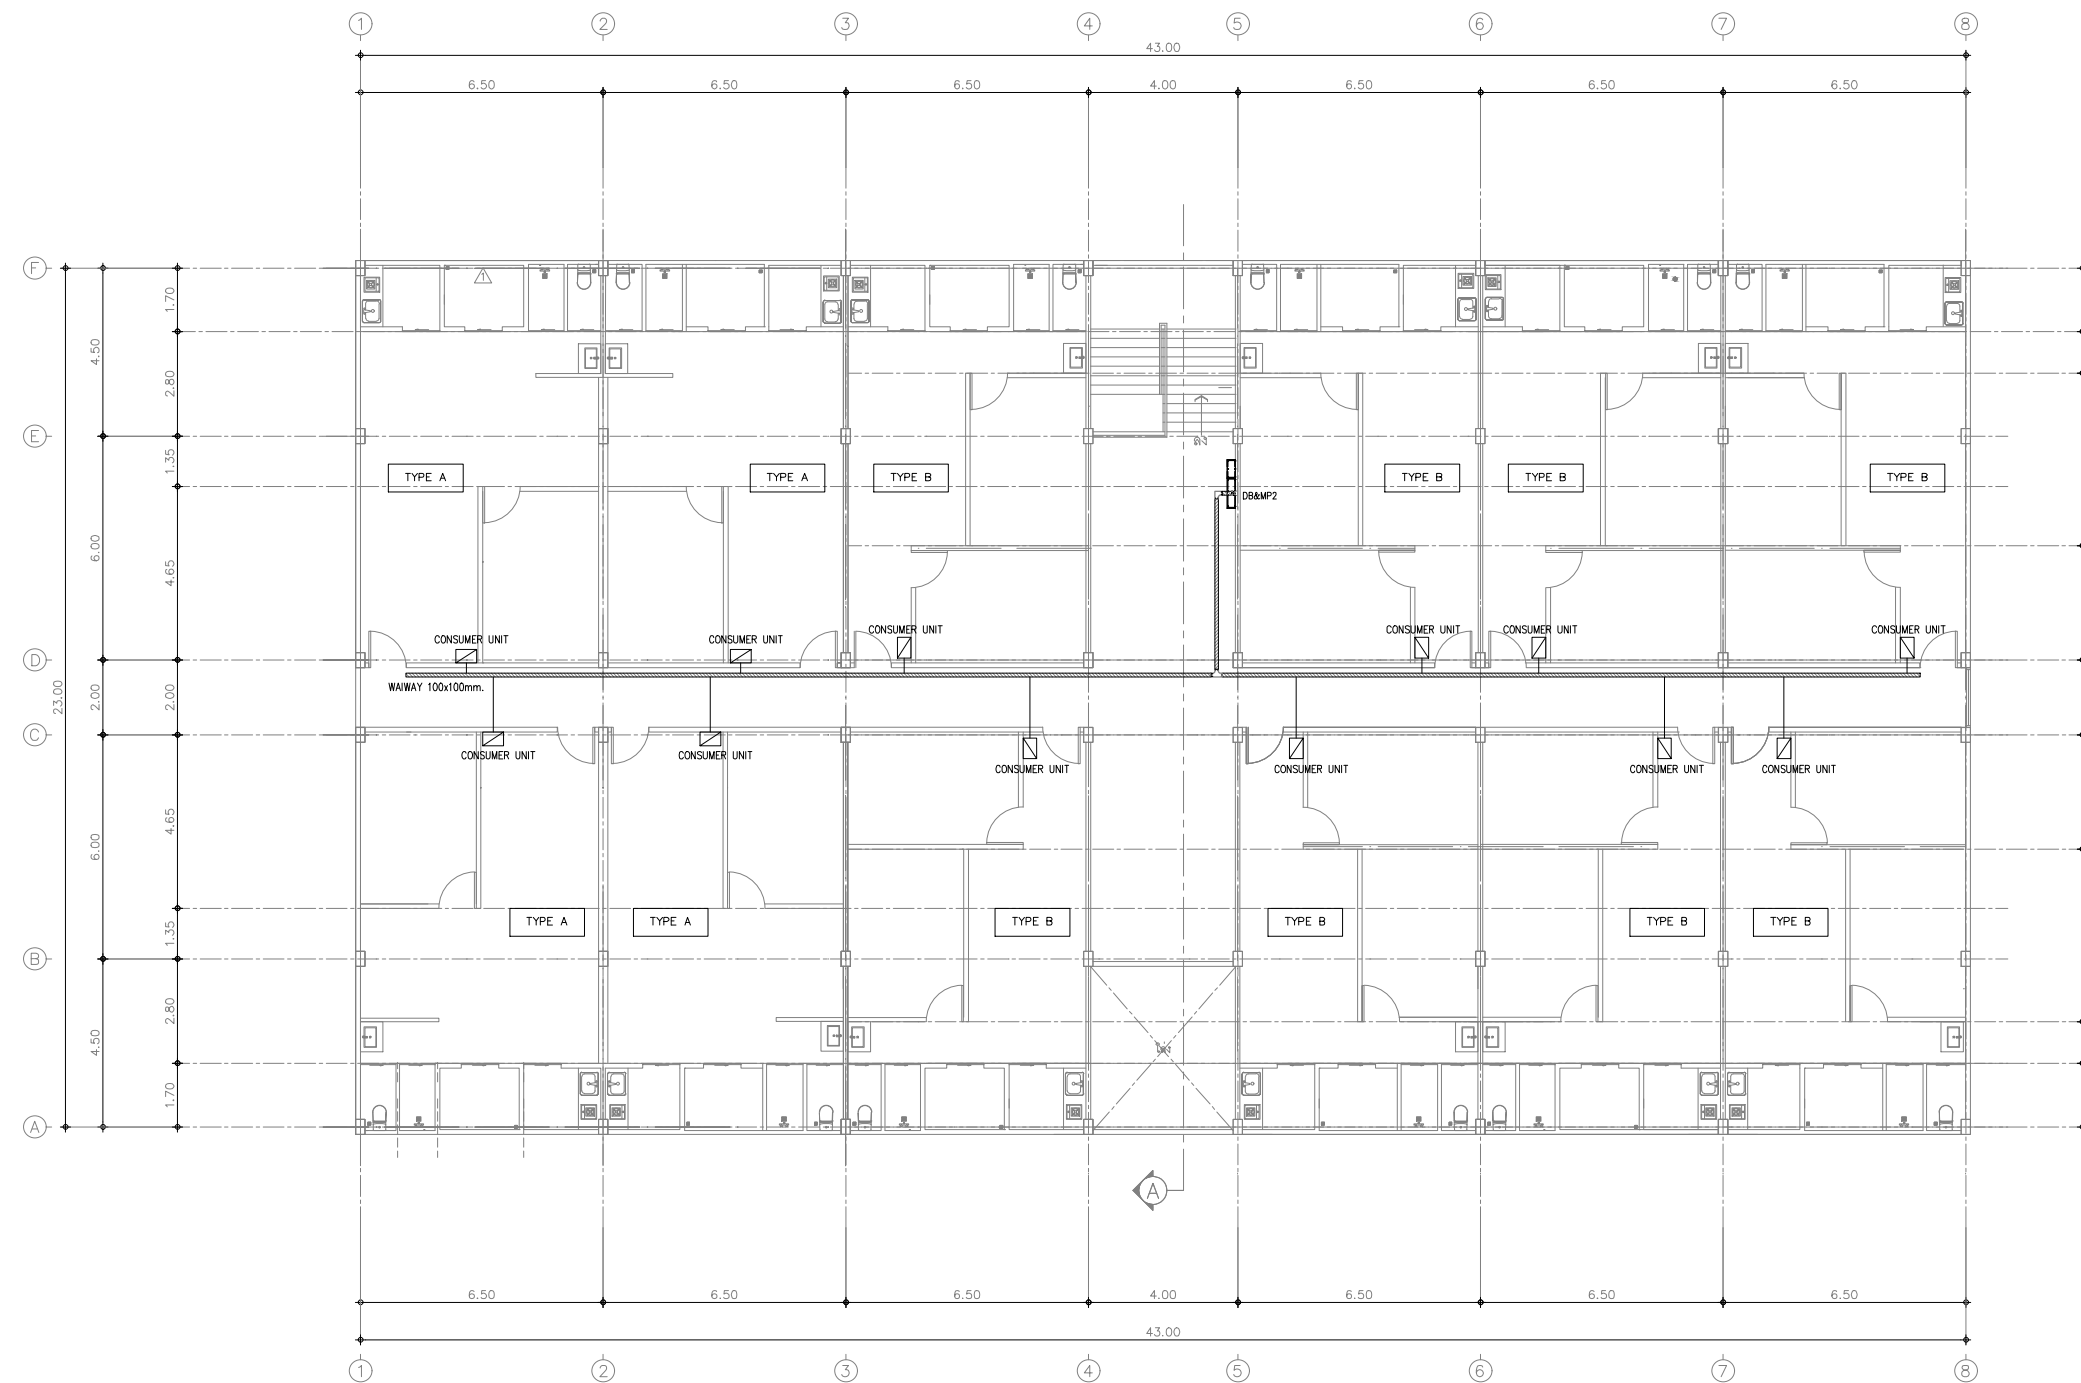

2 ND Floor Main Electrical Plan
Scale 1:100




PROJECT :
2-storey apartment
(Building A)

OWNER :
UNITECH PCB (THAILAND)
LOCATION :
Chorakhe Rong Chaiyo Ang Thong Province, Thailand

STRUCTURAL ENGINEER : นายชานนท์ สงวนวงศ์ สย 4227
333 หมู่ 3 ต.ปากคลองบางปลากด อ.พระสมุทรเจดีย์ จ.สมุทรปราการ
ARCHITECT : นายสุรชัย วาณิช ส-สด 3003
139/13 ซอยลาดพร้าว 41 แขวงจันทราภิรม เขตจตุจักร กรุงเทพมหานคร

ELECTRICAL ENGINEER :
SANITARY ENGINEER :

DRAWING NO. :
EE-008
REMARK :
FOR CONSTRUCTION

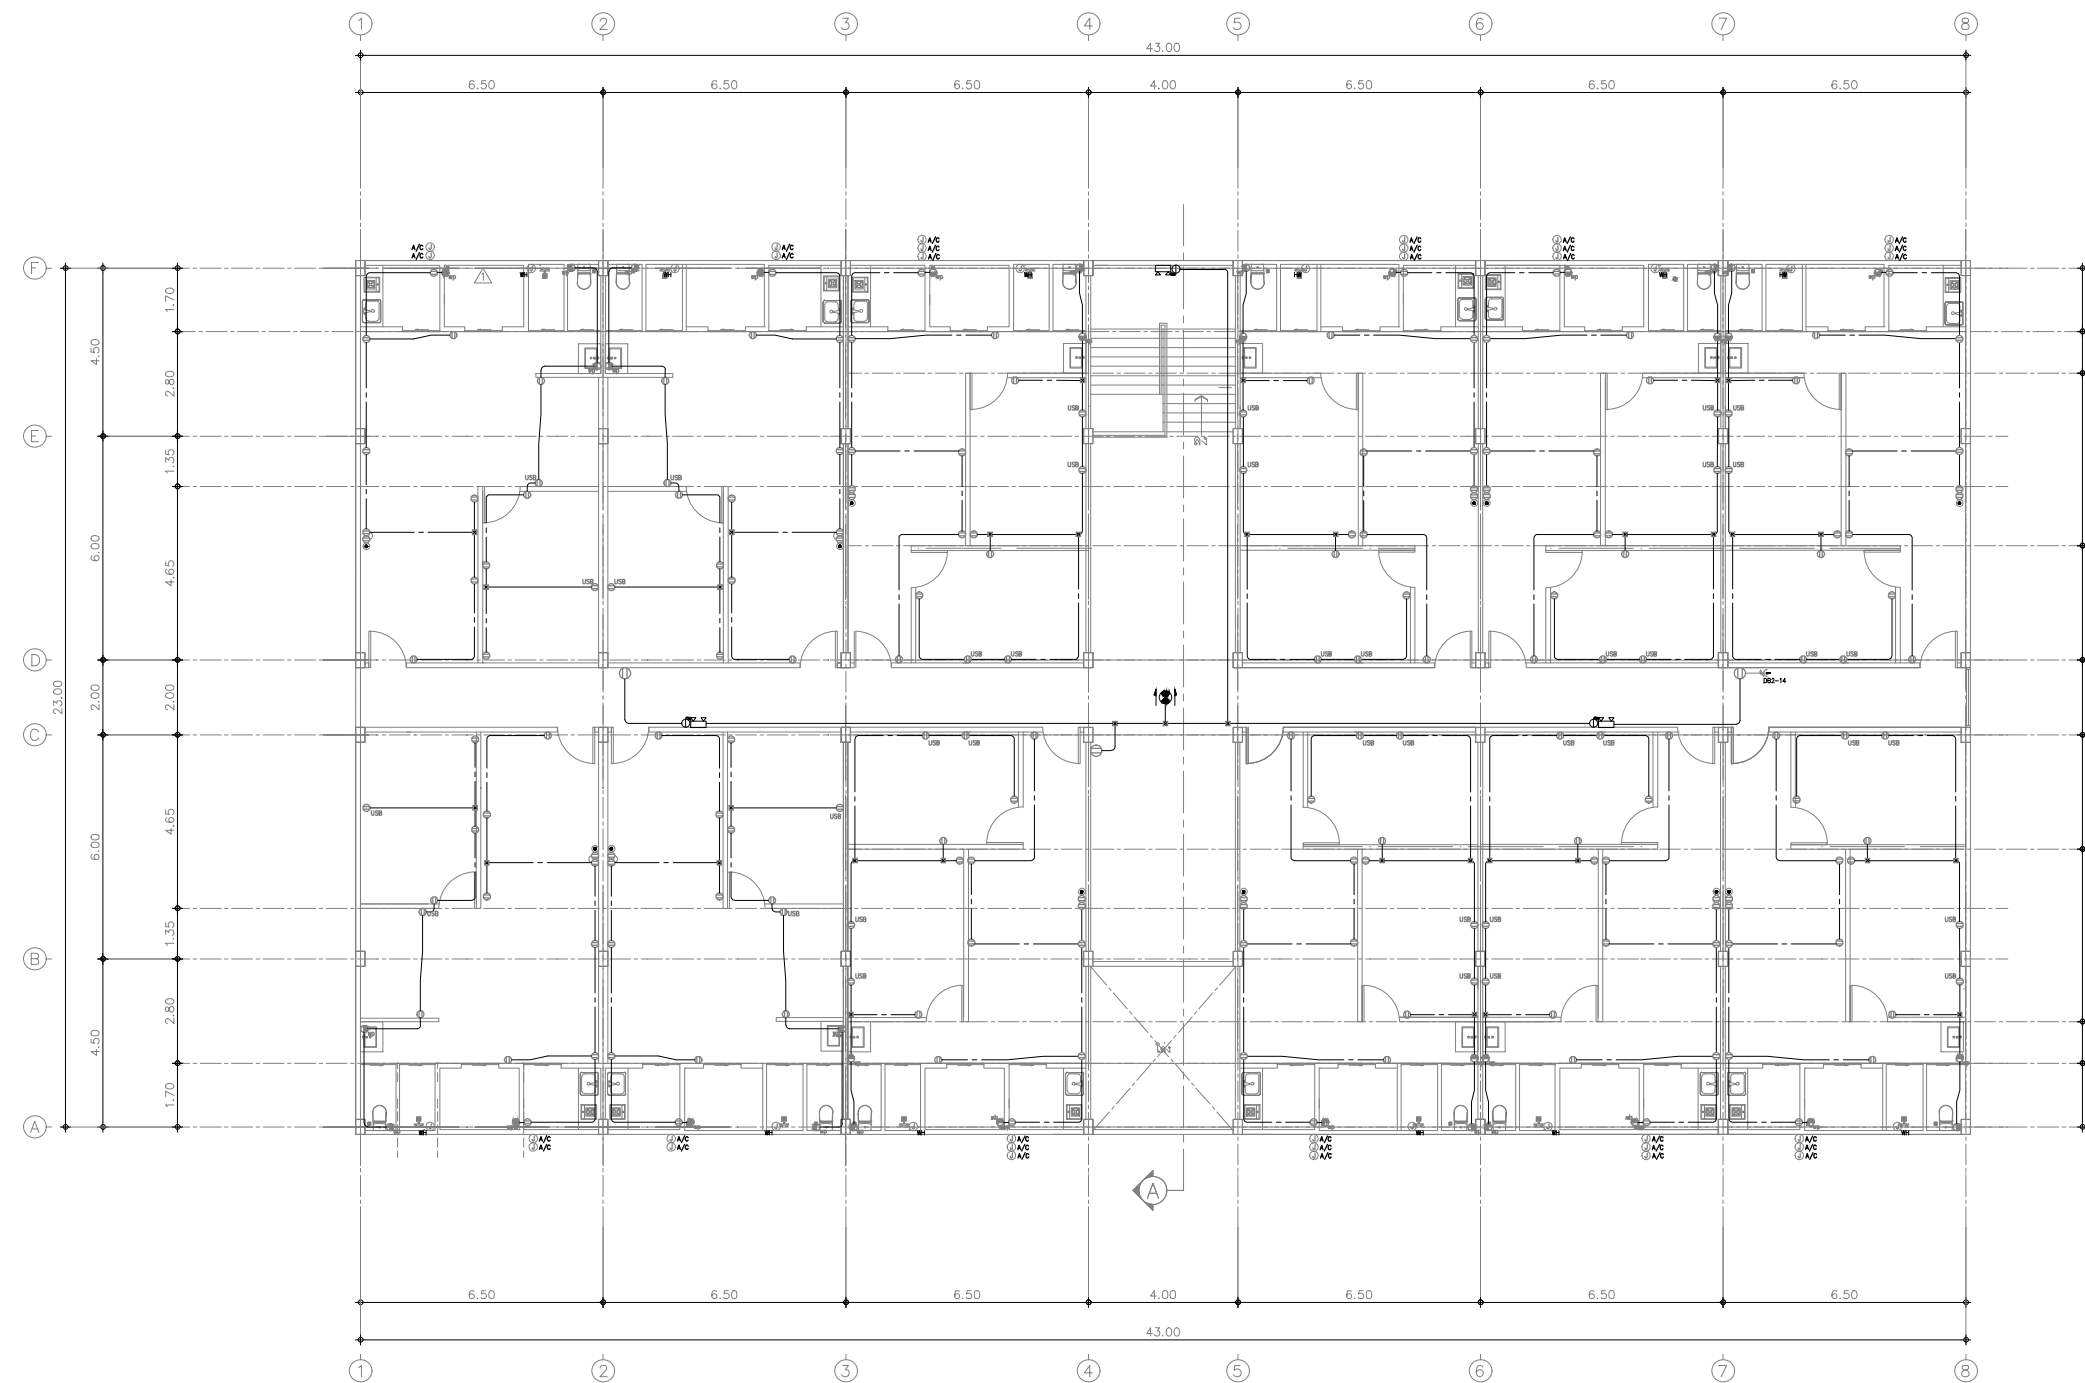

2 ND Floor Power Outlet Plan
Scale 1:100




PROJECT :
2-storey apartment
(Building A)

OWNER :
UNITECH PCB (THAILAND)
LOCATION :
Chorakhe Rong Chaiyo Ang Thong Province, Thailand

STRUCTURAL ENGINEER : นายชานนท์ สงวนวงศ์ สย 4227
333 หมู่ 3 ต.ปากคลองบางปลากด อ.พระสมุทรเจดีย์ จ.สมุทรปราการ
ARCHITECT : นายสุรชัย วาณิช ส-สด 3003
139/13 ซอยลาดพร้าว 41 แขวงจันทราภิรม เขตจตุจักร กรุงเทพมหานคร

ELECTRICAL ENGINEER :
SANITARY ENGINEER :

DRAWING NO. :
EE-009
REMARK :
FOR CONSTRUCTION

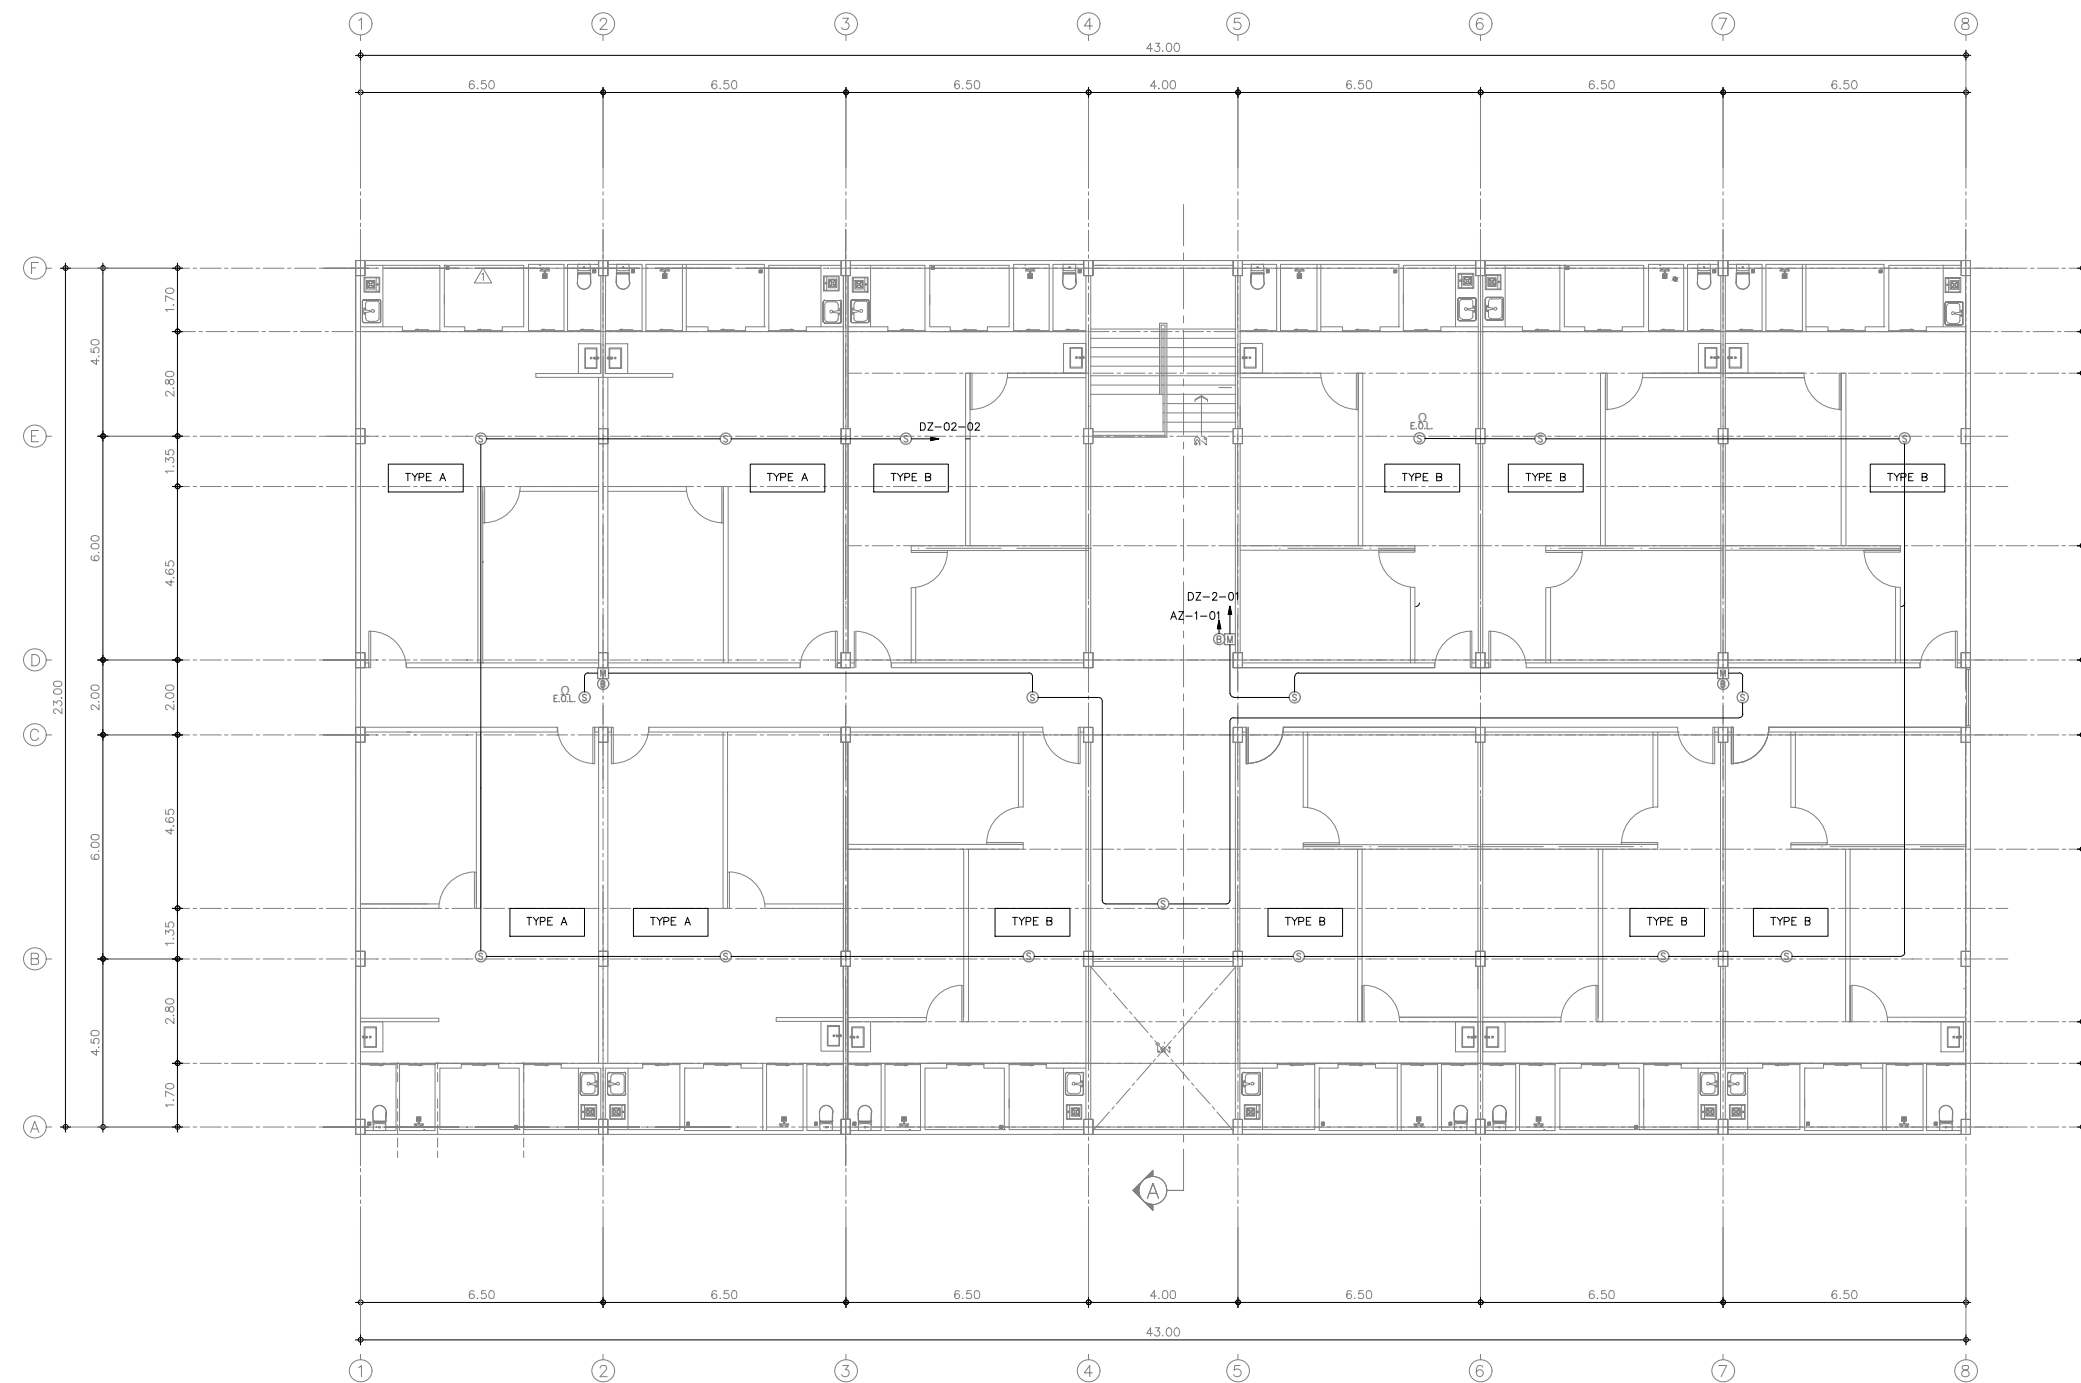

2 ND Floor Fire Alarm Plan
Scale 1:100




PROJECT :
2-storey apartment
(Building A)

OWNER :
UNITECH PCB (THAILAND)
LOCATION :
Chorakhe Rong Chaiyo Ang Thong Province, Thailand

STRUCTURAL ENGINEER : นายชานนท์ สงวนวงษ์ สย 4227
333 หมู่ 3 ต.ปากคลองบางปลากด อ.พระสมุทรเจดีย์ จ.สมุทรปราการ
ARCHITECT : นายสุรชัย วาณิช ส-สด 3003
139/13 ซอยลาดพร้าว 41 แขวงจันทรมาน เขตจตุจักร กรุงเทพมหานคร

ELECTRICAL ENGINEER :
SANITARY ENGINEER :

DRAWING NO. :
EE-010
REMARK :
FOR CONSTRUCTION

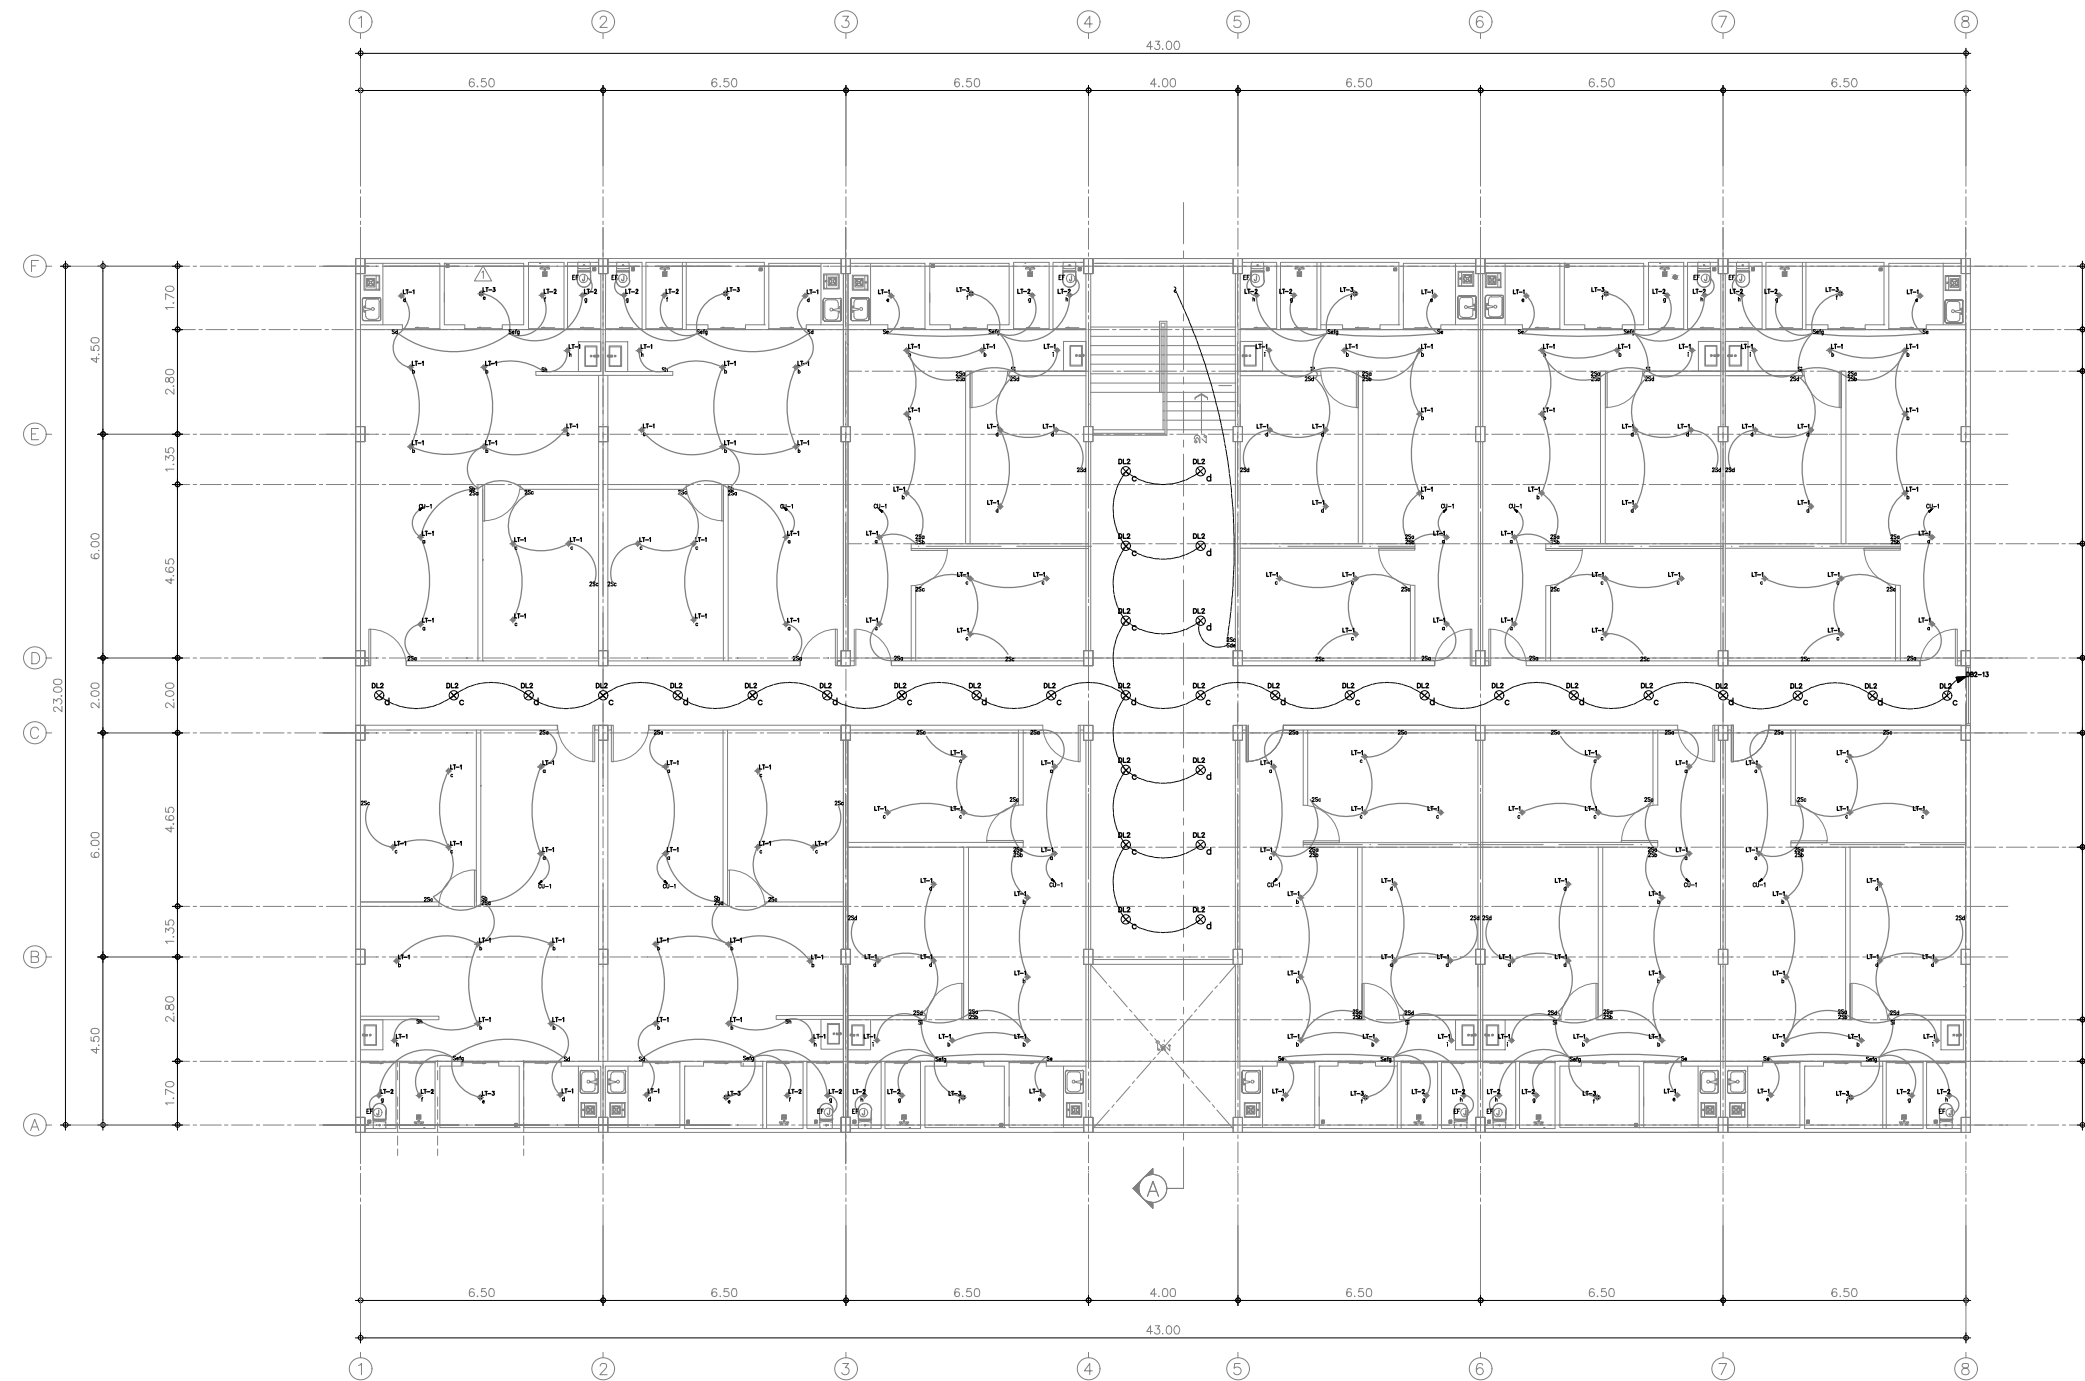

2 ND Floor Lighting Plan
Scale 1:100




PROJECT :
2-storey apartment
(Building A)

OWNER :
UNITECH PCB (THAILAND)
LOCATION :
Chorakhe Rong Chaiyo Ang Thong Province, Thailand


STRUCTURAL ENGINEER : นายชานนท์ สงวนวงศ์ สย 4227
333 หมู่ 3 ต.ปากคลองบางปลากด อ.พระสมุทรเจดีย์ จ.สมุทรปราการ
ARCHITECT : นายสุรชัย วานิชดี ส-สด 3003
139/13 ซอยลาดพร้าว 41 แขวงจันทราภิรม เขตจตุจักร กรุงเทพมหานคร

ELECTRICAL ENGINEER :
SANITARY ENGINEER :


DRAWING NO. :
EE-011
REMARK :
FOR CONSTRUCTION

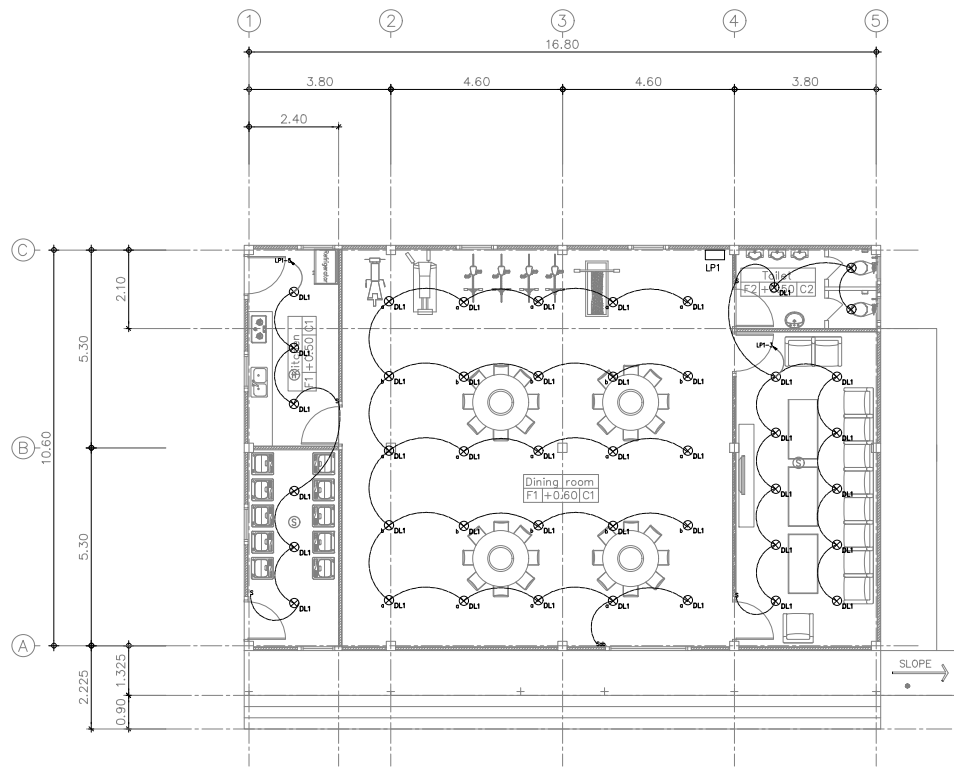


Lighting Plan DINING ROOM
Scale 1:100

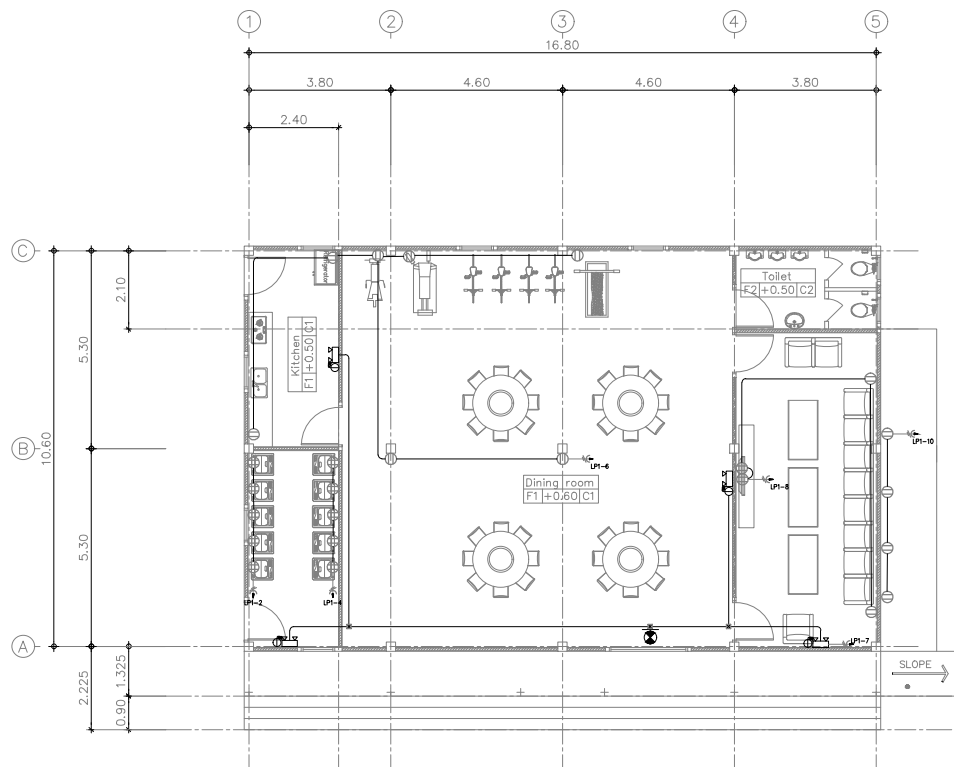

Power Outlet Plan DINING ROOM
Scale 1:100

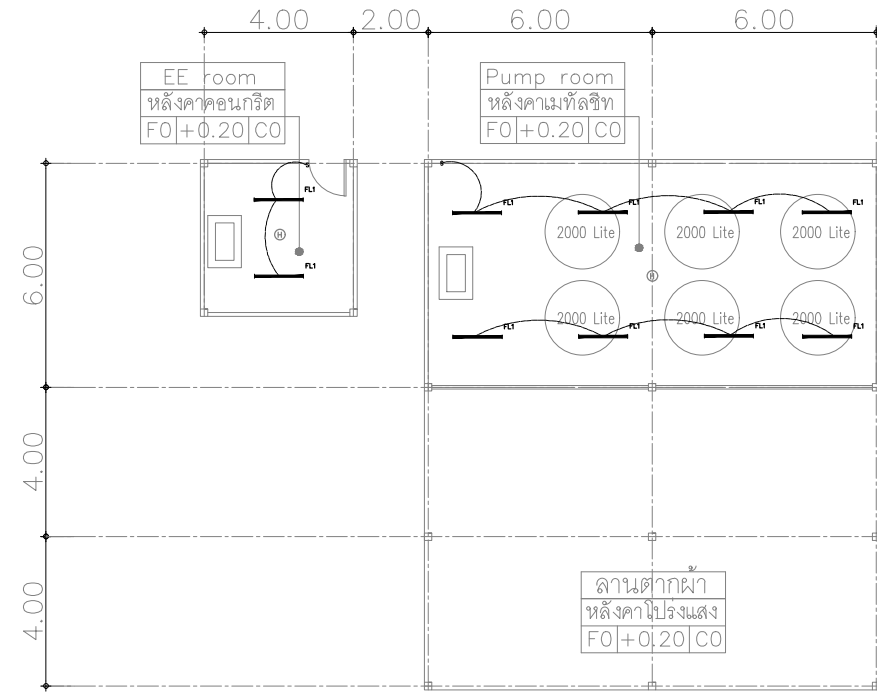

Lighting Plan EE-room, Pump room
Scale 1:100

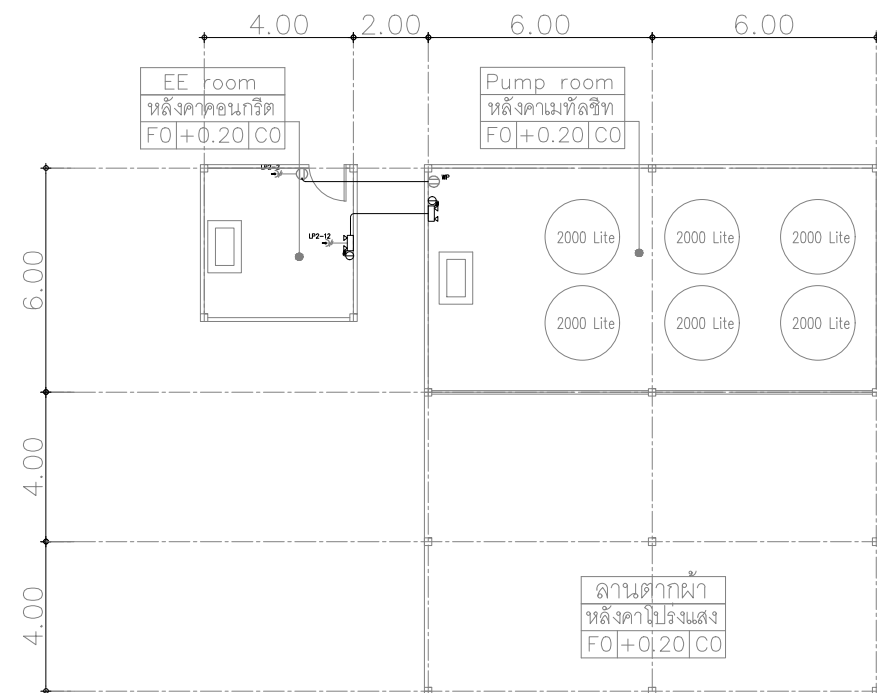

Power Outlet Plan EE-room, Pump room
Scale 1:100




PROJECT :
Canteen, EE-room, Pump room

OWNER :
UNITECH PCB (THAILAND)
LOCATION :
Chorakhe Rong Chaiyo Ang Thong Province, Thailand


STRUCTURAL ENGINEER : นายชานนท์ สงวนวงษ์ สย 4227
333 หมู่ 3 ต.ปากคลองบางปลากด อ.พระสมุทรเจดีย์ จ.สมุทรปราการ
ARCHITECT : นายสุรชัย วาณิช ส-สด 3003
139/13 ซอยลาดพร้าว 41 แขวงจันทน์นาคราช เขตจตุจักร กรุงเทพมหานคร

ELECTRICAL ENGINEER :
SANITARY ENGINEER :

DRAWING NO. :
EE-012
REMARK :
FOR CONSTRUCTION

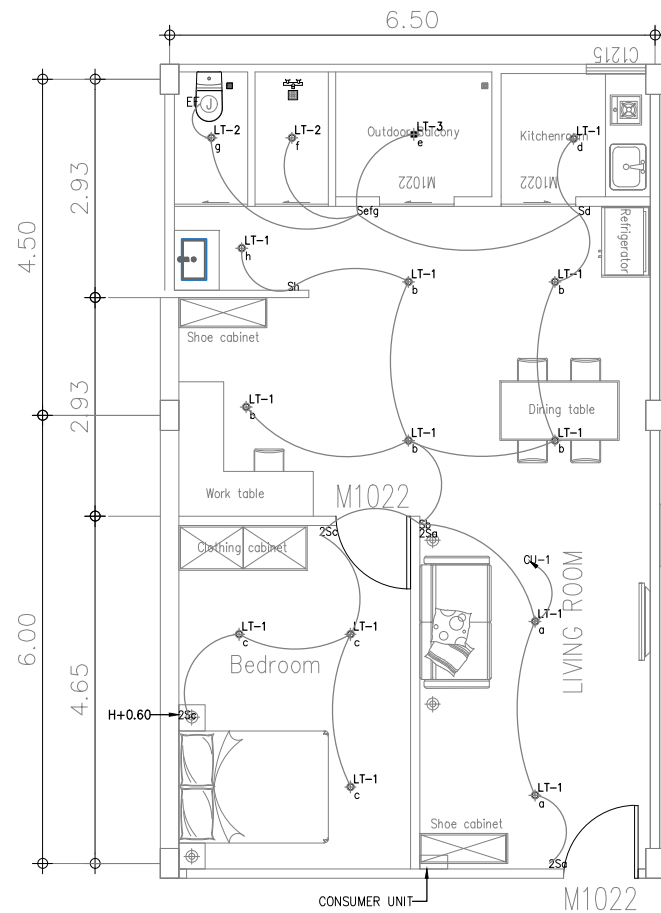


01 แปลนระบบไฟฟ้าแสงสว่างห้องพัก TYPE A

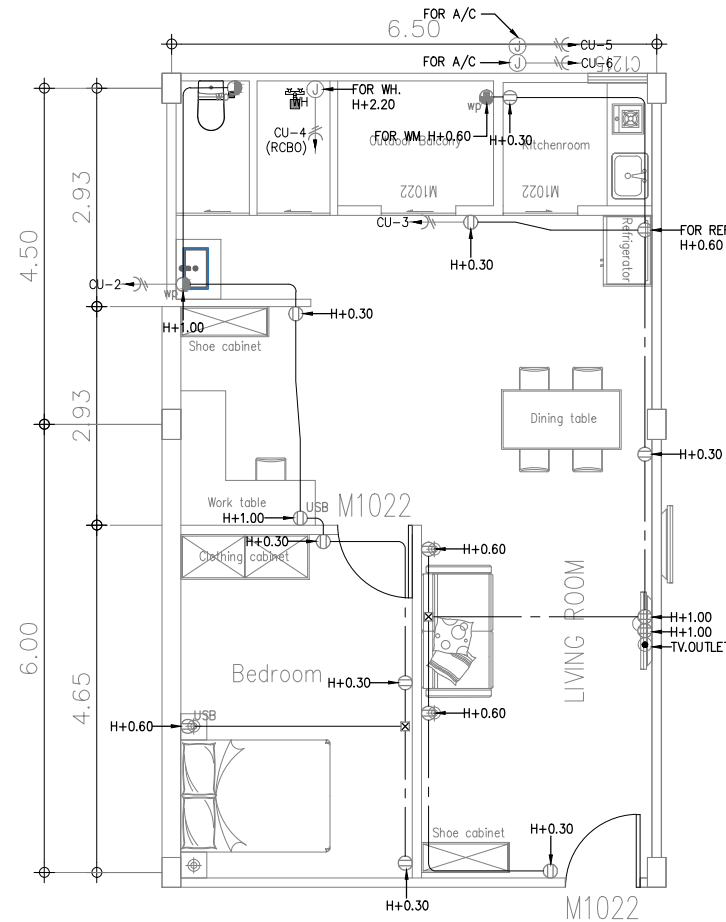

02 แปลนระบบตัวรับไฟฟ้าโทรทัศน์ห้องพัก TYPE A


SYMBOLS & ABBREVIATION	
SYMBOL	DESCRIPTION
	CONSUMER UNIT WITH MAIN CB.,8-12 CKT.
	DOWNLIGHT (SPEC BY INTERIOR DESIGN)
	DOWNLIGHT (SPEC BY INTERIOR DESIGN)
	DOWNLIGHT SURFACE (SPEC BY INTERIOR DESIGN)
	SIMPLEX OUTLET +0.30 m. AFF (SPEC BY INTERIOR DESIGN)
	DUPLEX OUTLET +0.30 m. AFF (SPEC BY INTERIOR DESIGN)
	SIMPLEX OUTLET WEATHER PROOF +0.30 m. AFF (SPEC BY INTERIOR DESIGN)
	DUPLEX OUTLET +USB.+TYPE C. +0.30 m. AFF (SPEC BY INTERIOR DESIGN)
	TV JACK OUTLET (SPEC BY INTERIOR DESIGN)
	JUNCTION BOX

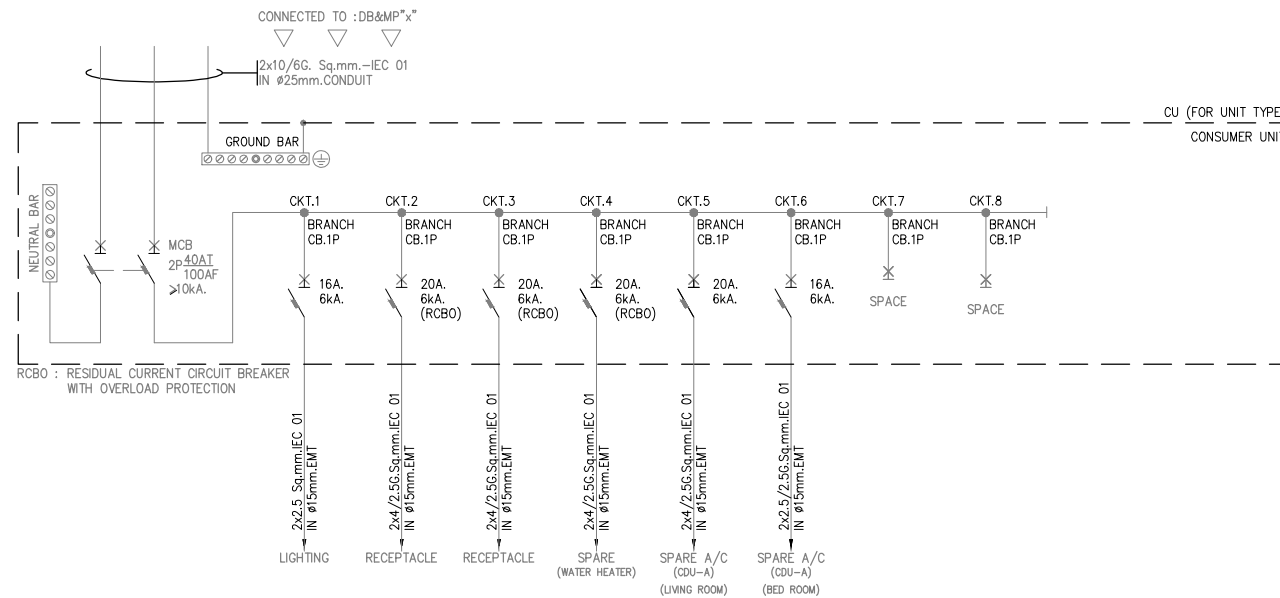


03 ไดอะแกรมเส้นเดียวตัว CU TYPE A
NTS




PROJECT :	อาคาร ค.ส.ล. 2 ชั้น (อาคาร A)	OWNER :	บริษัท อุตสาหกรรม (ไทยแลนด์) จำกัด	STRUCTURAL ENGINEER :	นายอานนท์ สงวนวงษ์ สช. 4227 333 หมู่ 3 ต.ปากคลองบางปลากด อ.พระสมุทรเจดีย์ จ.สมุทรปราการ	ELECTRICAL ENGINEER :		DRAWING NO. :	EE-13
		LOCATION :	ตำบลจระเข้ทอง อำเภอไชโย จังหวัดอ่างทอง	ARCHITECT :	นายสุรชัย วานิชดี ส.ส.ด 3003 139/13 ซอยลาดพร้าว 41 แขวงจันทราภิรม เขตจตุจักร กรุงเทพมหานคร	SANITARY ENGINEER :		REMARK :	FOR CONSTRUCTION

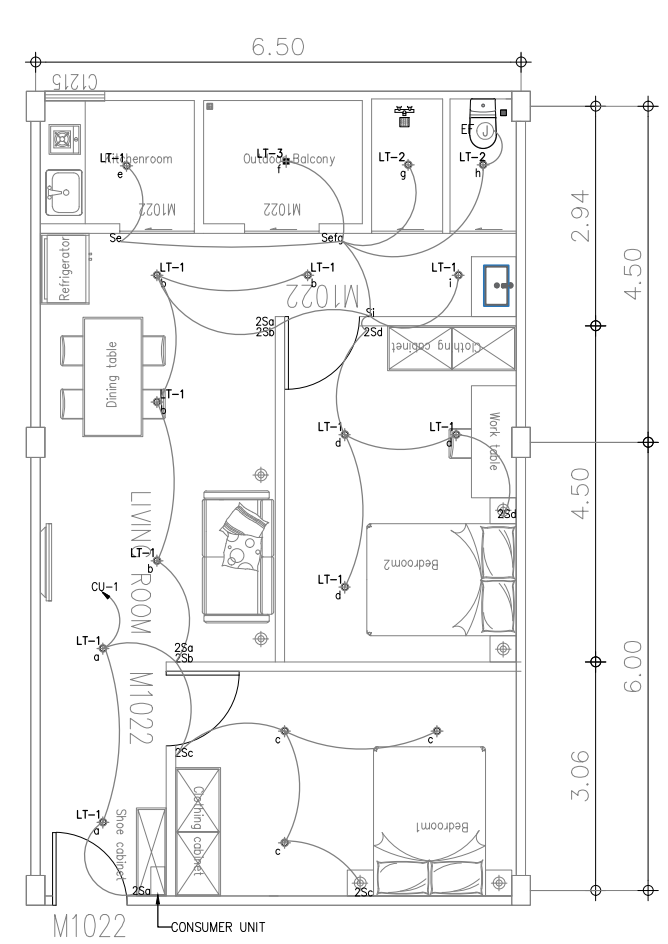

01 แผนระบบไฟฟ้าแสงสว่างห้องพัก TYPE B

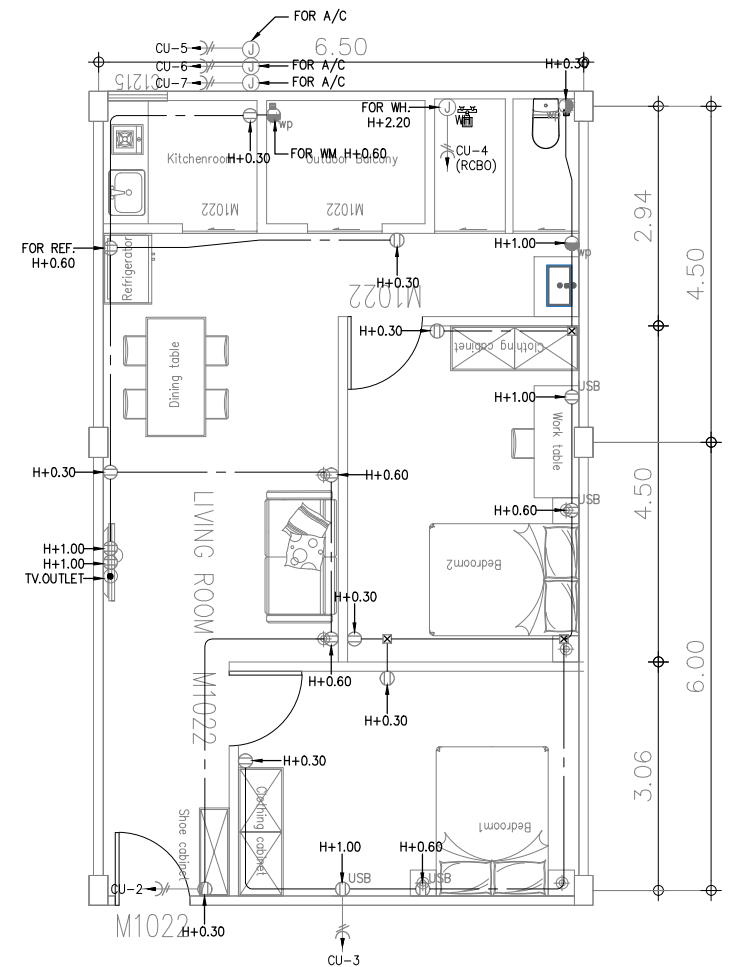

02 แผนระบบเดินไฟฟ้าโทรทัศน์ห้องพัก TYPE B

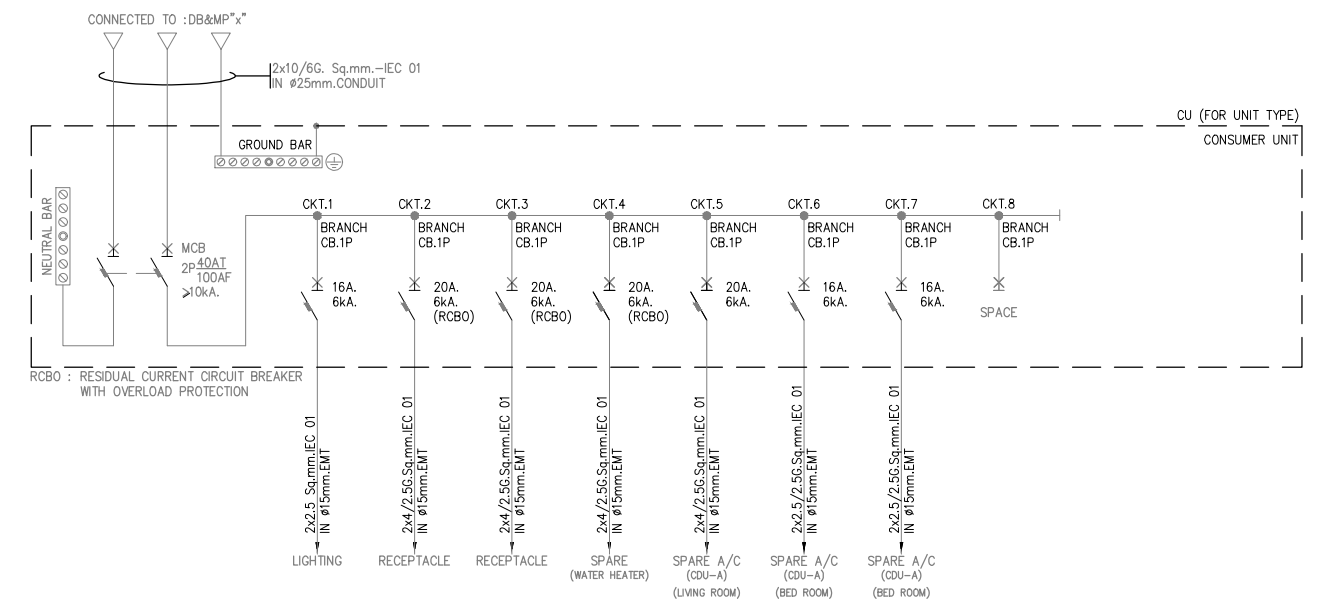

03 ไดอะแกรมเดินด้วยตู้ CU TYPE B

SYMBOLS & ABBREVIATION	
SYMBOL	DESCRIPTION
	CONSUMER UNIT WITH MAIN CB, 8-12 CKT.
	DOWNLIGHT (SPEC BY INTERIOR DESIGN)
	DOWNLIGHT (SPEC BY INTERIOR DESIGN)
	DOWNLIGHT SURFACE (SPEC BY INTERIOR DESIGN)
	SIMPLEX OUTLET +0.30 m. AFF (SPEC BY INTERIOR DESIGN)
	DUPLEX OUTLET +0.30 m. AFF (SPEC BY INTERIOR DESIGN)
	SIMPLEX OUTLET WEATHER PROOF +0.30 m. AFF (SPEC BY INTERIOR DESIGN)
	DUPLEX OUTLET +USB+TYPE C. +0.30 m. AFF (SPEC BY INTERIOR DESIGN)
	TV JACK OUTLET (SPEC BY INTERIOR DESIGN)
	JUNCTION BOX